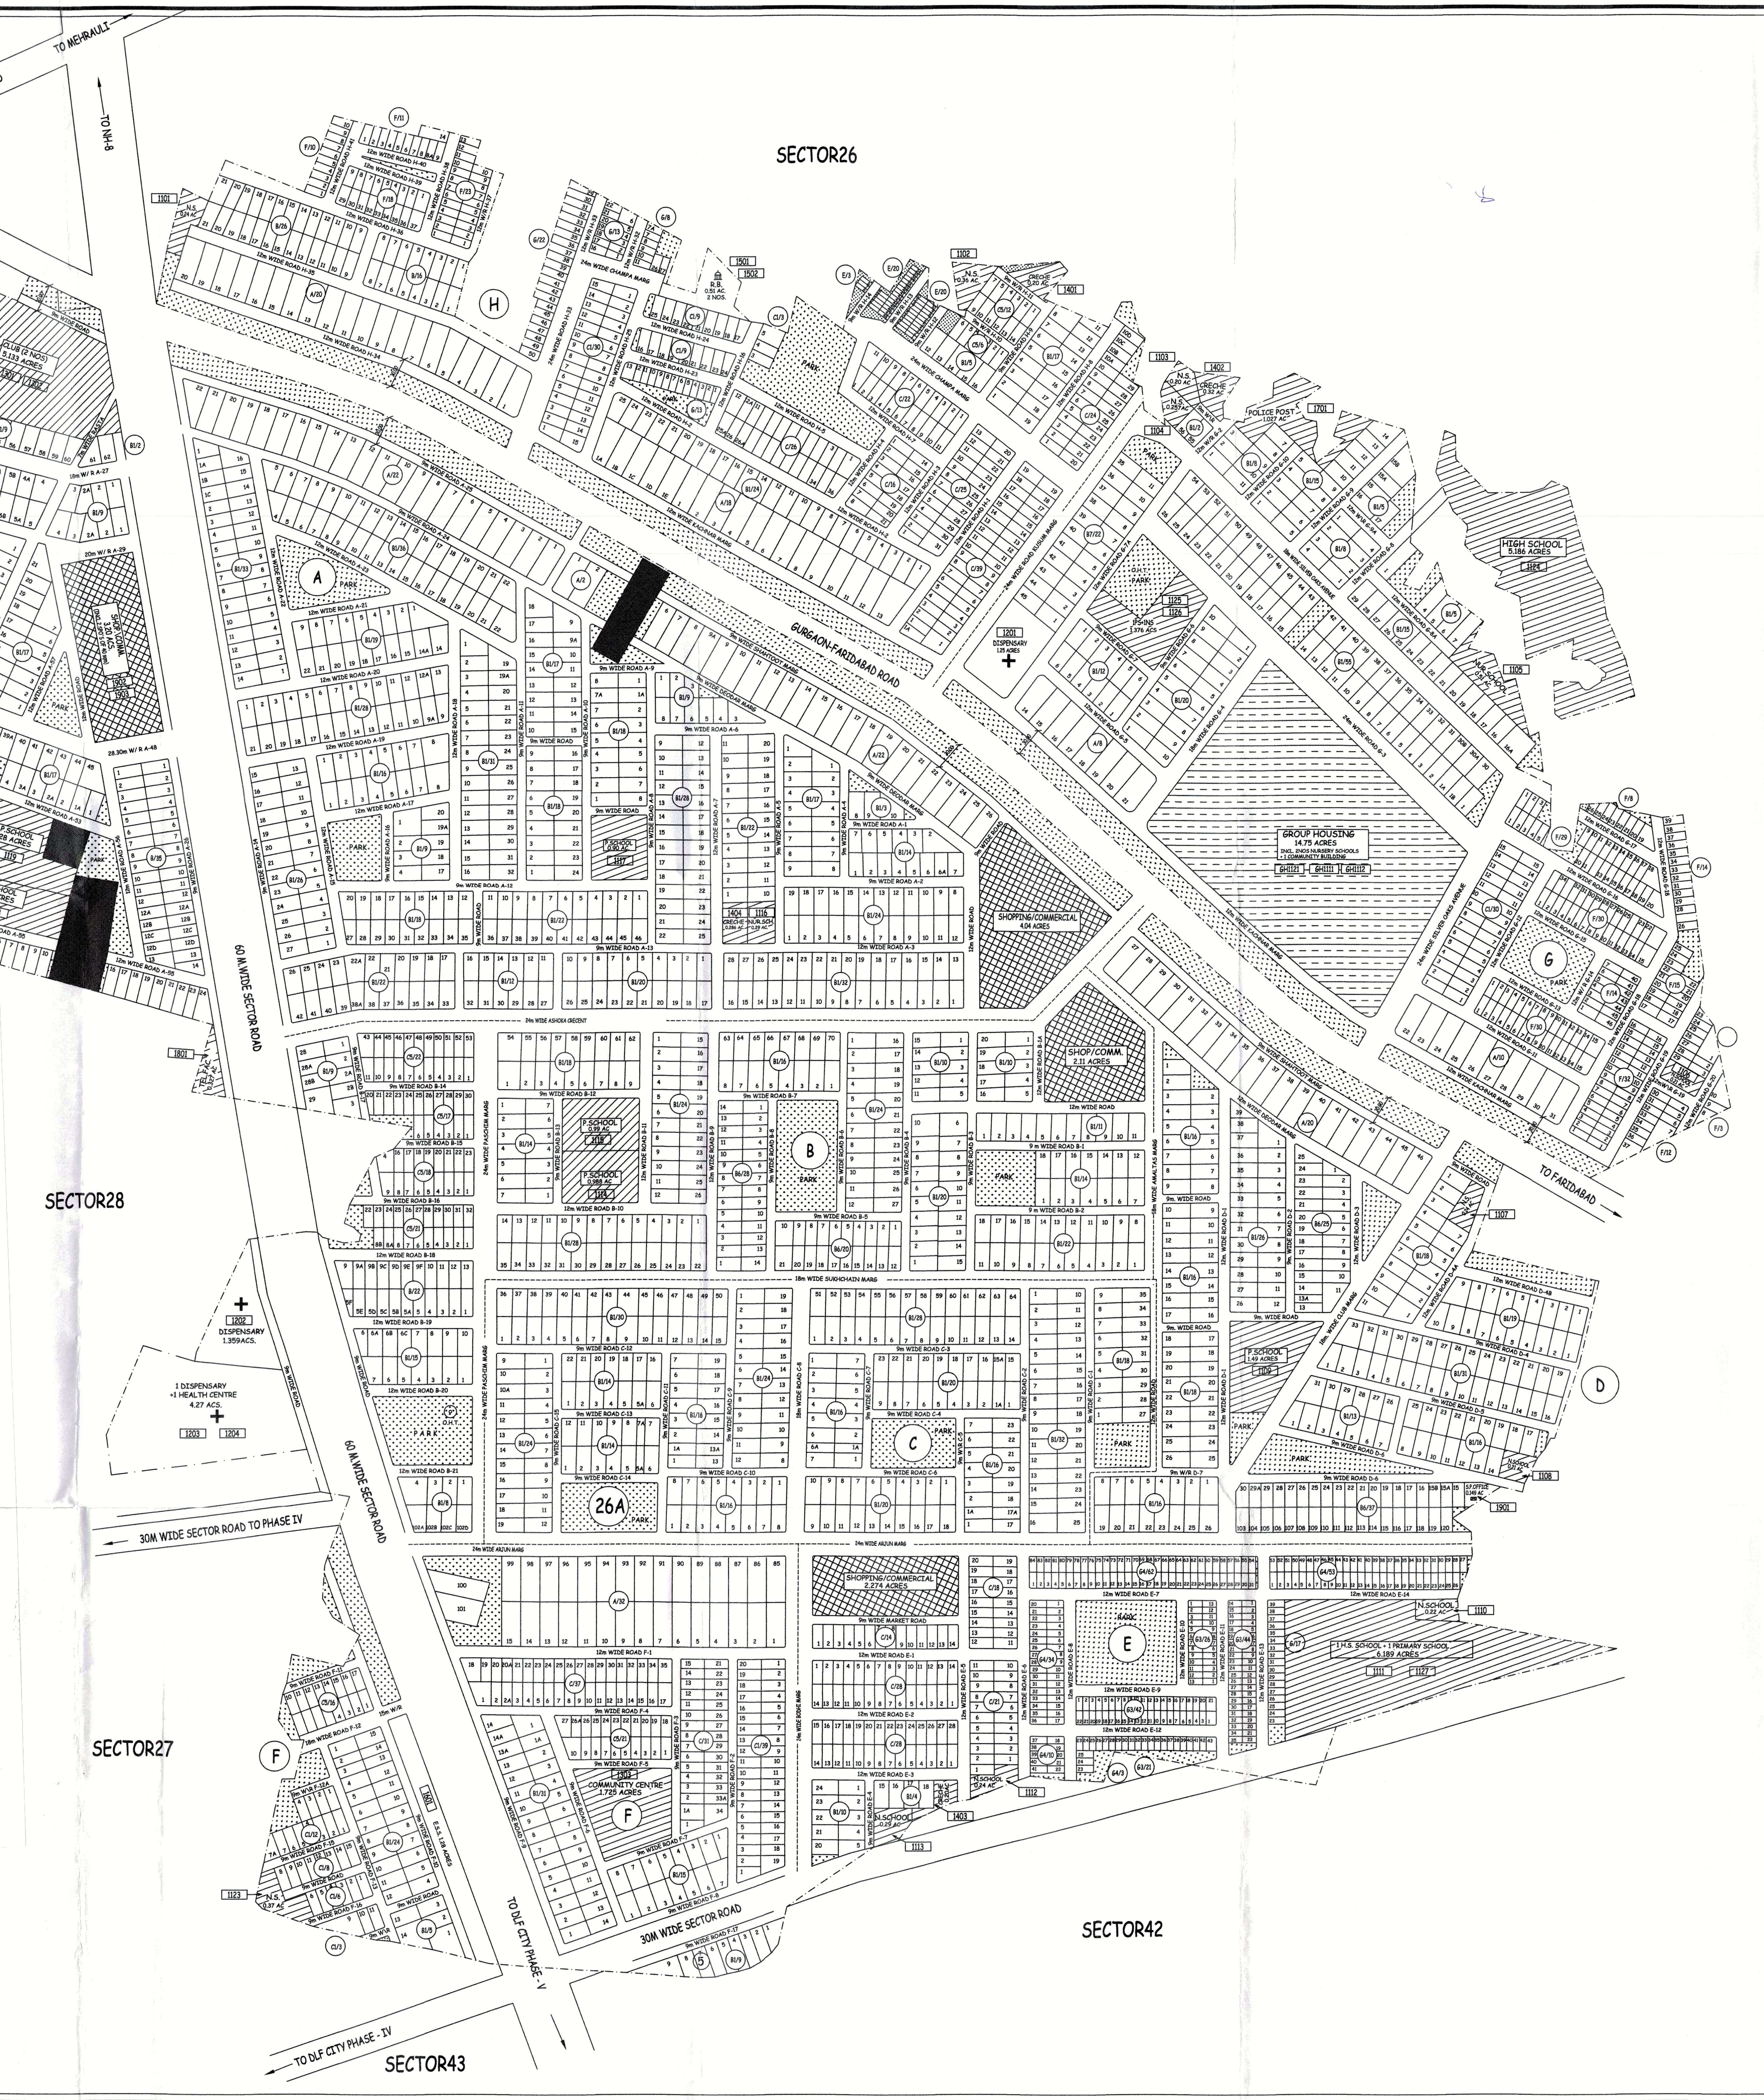

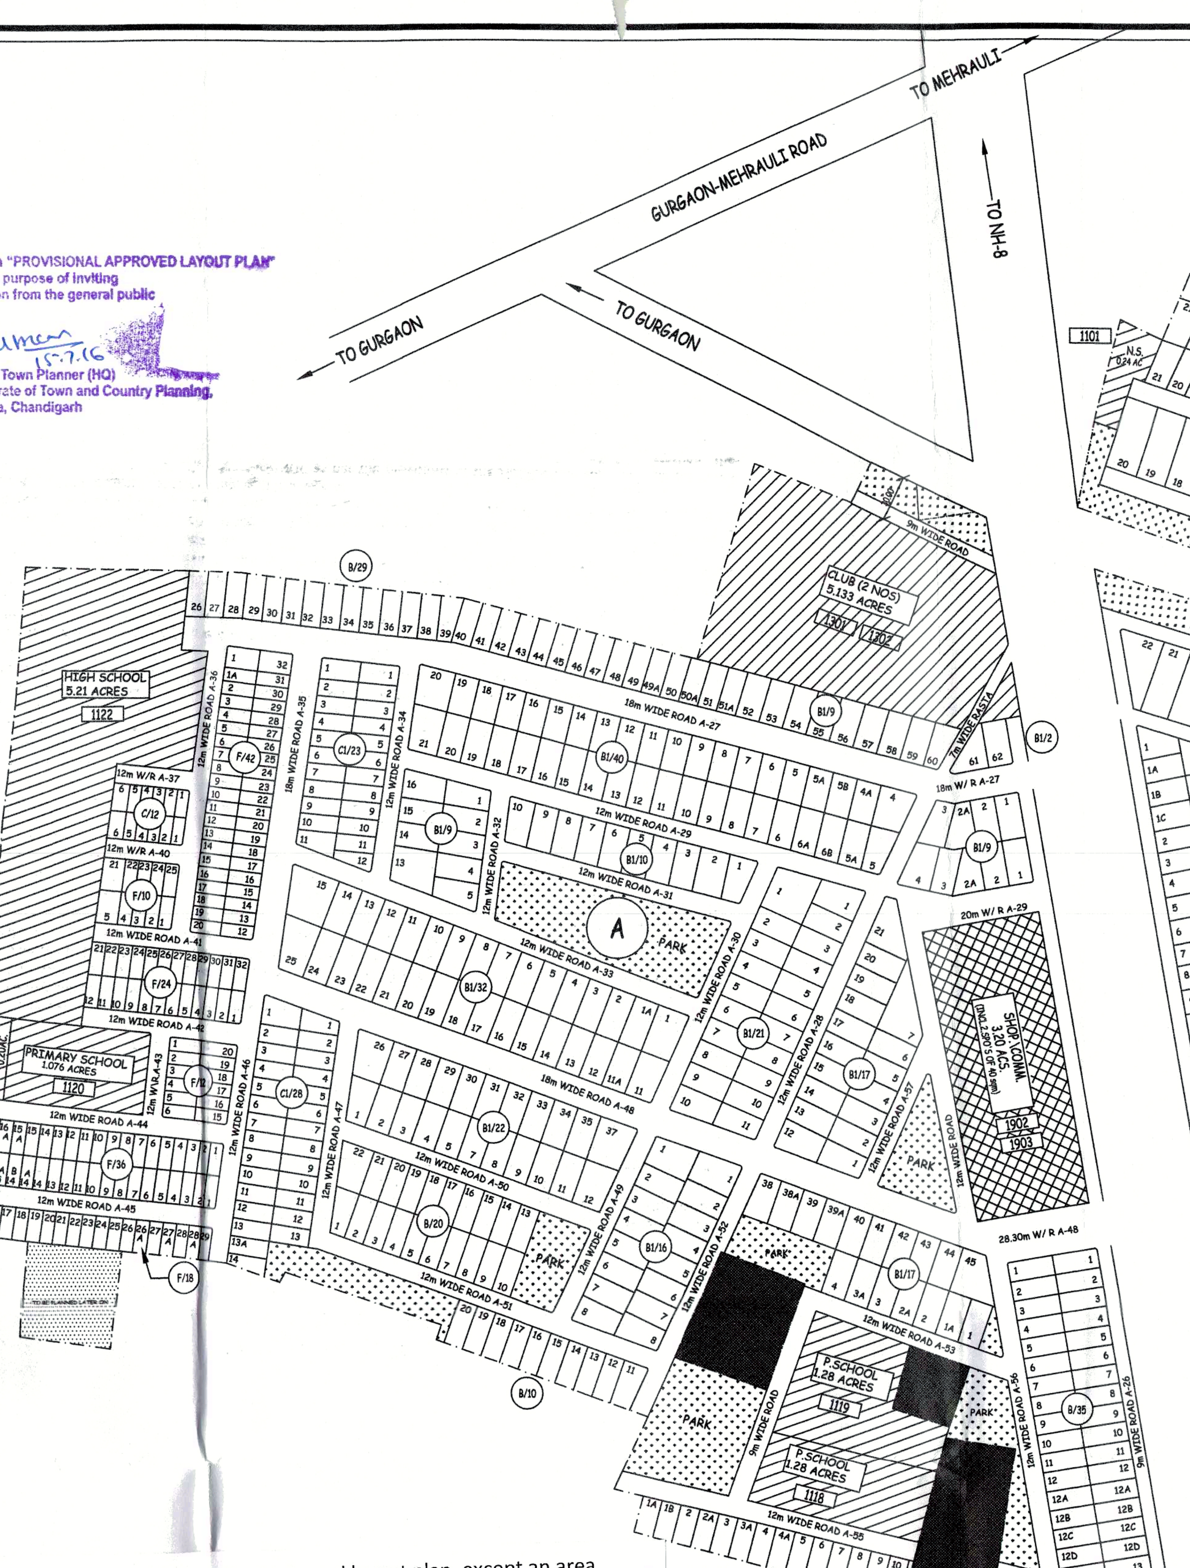

This is a "PROVISIONAL APPROVED LAYOUT PLAN" only for purpose of inviting objection from the general public

District Town Planner (HQ)
Directorate of Town and Country Planning,
Haryana, Chandigarh

There is no change from the earlier approved layout plan, except an area measuring 3.43 acres in Phase-III is proposed to de-licence.

That this revised Layout plan for an area of 1538.668 acres (Drg. No. DG,TCP-5572-I,II & III dated 09.06.2016) comprised of licenses which were issued in respect of Residential Plotted Colony DLF City, Phase-I, II & III being developed by DLF Limited and others Gurgaon Manesar Urban Complex is hereby approved subject to the following conditions:-

1. That this revised Layout plan shall be read in conjunction with the clauses appearing on the agreement executed under Rule 11 and the bilateral agreement.
2. That the plotted area of the colony shall not exceed 55% of the net planned area of the colony. The entire area reserved for commercial purposes shall be taken as plotted for calculation of the area under plots.
3. That the demarcation plans as per site of all the residential, commercial and institutional sites shall be got approved from this Department and construction on these sites shall be governed by the Punjab Scheduled Roads and Controlled Areas Restriction of Unregulated Development Rules, 1965 and the Zoning Plan approved by the Director General, Town & Country Planning, Haryana.
4. That if any high-tension lines passing in the colony area shall have to be suitably aligned or right of way along the same shall be maintained as per ISI norms.
5. That for proper planning and integration of services in the area adjacent to the colony, the colonizer shall abide by the directions of the DG,TCP for the modification of layout plans of the colony.
6. That the revenue rasta falling in the colony shall be kept free for circulation/movement as shown in the layout plan.
7. That the colonizer shall abide by the directions of the DG,TCP, Haryana and accordingly shall make necessary changes in the layout plan for making any adjustment in the alignment of the peripheral roads, internal road circulation or for proper integration of the planning proposals of the adjoining areas of the sectors as shown on the Development Plan.
8. That no property/plot shall derive access directly from the carriage way of 30 metres or more wide sector road.
9. All green belts provided in the layout plan within the licenced areas of the colony shall be developed by the colonizer. All other green belts outside the licenced area shall be developed by the Haryana Urban Development Authority/colonizer on the directions of the Director General, Town & Country Planning Haryana or in accordance with terms and conditions of the agreements of the licenses.
10. At the time of demarcation, if required percentage of NPNL/ EWS plots and the area under infrastructure are reduced, the same will be provided by the colonizer in the licenced area.
11. Any excess area over and above the permissible 4% under commercial use shall be deemed to be open space.
12. The maximum number of dwelling units in a plot shall be as per the provisions of the Rule 49 of the Rules, 1965. This condition shall also be incorporated in the zoning plan and in the allotment letters being issued by the colonizer to the plot holders. The stipulation shall also be incorporated in the agreement to be executed by the colonizer with the plot buyers.
13. The portion of the sector/development plan roads /green belts as provided in the Development Plan, which form part of the licenced area shall be transferred free of cost to the government on the lines of section 3(3)(a)(iii) of the Act No.8 of 1975.
14. That the odd size plots (except EWS plots which are approved of standard dimensions) are being approved subject to the conditions that these plots should not have a frontage of less than 75% of the standard frontage when demarcated and area of no plot shall exceed 2 kanals.
15. That you will have no objection to the regularization of the boundaries of the licence through give and take with the land that HUDA is finally able to acquire in the interest of planned development and integration of services. The decision of the competent authority shall be binding in this regard.
16. That the colonizer shall obtain the clearance from MoEF/SEIAA as per the provisions of the Notification No. S.O. 1533 (E) Dated 14.9.2006 issued by Ministry of Environment and Forest, Government of India, before starting the construction/execution of development works at site.
17. That the rain water harvesting system shall be provided as per Central Ground Water Authority norms/Haryana Govt. notification as applicable.
18. That you shall strictly comply with the directions issued vide notification No. 19/6/2016-5P dated 31.03.2016 issued by Haryana Government Renewable Energy Department.
19. That you shall ensure the installation of Solar Power Plant as per provisions of Haryana Solar Power policy, 2016 issued by Haryana Government Renewable Energy Department vide Notification No. 19/4/2016-5 Power dated 14.03.2016.
20. That you shall ensure the installation of Solar Photovoltaic Power Plant as per the provisions of order No. 22/52/2005-5 Power dated 21.03.2016 issued by Haryana Government Renewable Energy Department.
21. That you shall use only Light Emitting Diode lamps (LED) fitting for internal lighting as well as campus lighting.

(VIJAY KUMAR) DTP (HQ)
(DINESH SINGH CHAUHAN) STP (M) HQ
(KAMAL KUMAR) CTP (HR)
(ARUN KUMAR GUPTA, IAS) DG,TCP (HR)
(RAM AVTAR BASSI) AD (HQ)
(BALWANT SINGH) SD (HQ)
(PRIYAM SHARMA) ATP (HQ)

DLF BUILDING INDIA

DETAILS OF PLOTS

TYPE	SIZE WIDTH	SIZE DEPTH	AREA IN SQM.	PHASE I NOS.	PHASE I AREA IN SQM	PHASE II NOS.	PHASE II AREA IN SQM	PHASE III NOS.	PHASE III AREA IN SQM	TOTAL NOS.	TOTAL AREA IN SQM
A	19.00	45.00	855.00	154	131670.00	111	94905.00	35	29925.00	300	256500.00
A2	18.00	45.00	810.00	0	0	0	0.00	12	9720.00	12	9720.00
A3	18.00	40.00	720.00	0	0	0	0.00	12	8640.00	12	8640.00
A1	15.00	38.00	570.00	0	0	68	38760.00	0	0.00	68	38760.00
B2	13.50	35.00	472.50	0	0	58	27405.00	0	0.00	58	27405.00
B7	16.575	27.15	450.011	22	9900.24	0	0.00	0	0.00	22	9900.24
B4	13.00	32.50	422.50	0	0.00	0	0.00	28	11830.00	28	11830.00
B1	15.00	28.00	420.00	1707	716940.00	327	137340.00	624	262080.00	2658	1116360.00
B	12.00	28.00	336.00	181	60816.00	617	207312.00	235	78960.00	1033	347088.00
B6	12.00	25.00	300.00	110	33000.00	0	0	0	0	110	33000.00
C6	12.575	21.00	264.08	0	0	69	18221.52	0	0	69	18221.52
C1	11.00	24.00	264.00	200	52800.00	231	60984.00	737	194568.00	1168	308352.00
C	10.44	24.00	250.56	329	82434.24	758	189924.48	0		1087	272358.72
C5	10.00	22.50	225.00	133	29925.00	0	0	129	29025.00	262	58950.00
D	10.00	21.00	210.00	0	0	358	75180.00	0	0	358	75180.00
D1	8.56	21.00	179.76	0	0	340	61118.40	50	8988.00	390	70106.40
F	8.25	20.27	167.23	423	70737.23	211	35285.00	0	0	634	106022.24
G1	8.00	17.06	136.48	0	0	0	0	207	28251.36	207	28251.36
G	7.333	17.06	125.10	63	7881.30	80	10008.00	23	2877.30	166	20766.60
G6	6.60	18.95	125.07	0	0	0	0	334	41773.38	334	41773.38
G4	7.328	17.06	125.02	162	20253.24	0	0	0	0	162	20253.24
G3	6.50	14.02	91.13	133	12120.29	0	0	0	0	133	12120.29
E	4.00	12.50	50.00	0	0	0	0	698	34900.00	698	34900.00
E	4.00	12.50	50.00	43	2150.00	0	0	2426	121300.00	2469	123450.00
			TOTAL	3660	1230627.54	3228	956443.40	5550	862838.04	12438	3049908.99
		AREA IN ACRES			304.095		236.343		213.212		753.650

DETAILS OF AREAS

DESCRIPTION	PHASE-I	PHASE-II	PHASE-III	TOTAL	%AGE
TOTAL AREA OF LAND	590.097	488.004	460.567	1538.668	
TO BE PLANNED LATER ON	0.844	0	3.09	3.929	
AREA UNDER GROUP HOUSING	14.750	22.843	9.458	47.051	
NET PLANNED AREA	574.503	465.161	448.024	1487.688	
AREA UNDER PLOTS	304.095	236.343	213.212	753.650	50.66
AREA UNDER SHOPPING/COMMERCIAL	11.624	9.161	38.330	59.115	3.97
TOTAL SALEABLE AREA	**315.719**	**245.504**	**251.542**	**812.765**	**54.63**

DETAILS OF AREAS UNDER SHOPPING / COMMERCIAL SITES

PHASE-I	3.20 + 2.11 + 2.274 + 4.04 =	11.624
PHASE-II	0.27 + 5.78 + 1.161 + 1.95 =	9.161
PHASE-III	33.00 + 0.328 + 1.152 + 0.20 + 3.65 =	38.330
TOTAL	=	59.115 Acres

DETAILS OF NEW PLOTS

TYPE	PHASE-I OLD	PHASE-I NEW	PHASE-I TOTAL	PHASE-II OLD	PHASE-II NEW	PHASE-II TOTAL	PHASE-III OLD	PHASE-III NEW	PHASE-III TOTAL	TOTAL OLD	TOTAL NEW	TOTAL TOTAL	%AGE
GENERAL	2703	0	2703	2239	0	2239	1705	-22	1683	6647	-22	6625	
N.P.N.L	781	8	789	989	0	989	1441	0	1441	3211	0	3211	25.82%
E.W.S.	176		176				2426		2426	2602		2602	20.92%
TOTAL	3660	8	3668	3228	0	3228	5572	0	5550	12460	-22	12438	

POPULATION ACHIEVED IN PLOTTED COLONY

PHASE-I	(3616 x 9) + (44 x 13.5) =	33138 Persons
PHASE-II	(3157 x 9) + (63 x 13.5) + (8 x 13.5) =	29372 Persons
PHASE-III	(5432 x 9) + (30 x 13.5) + (110 x 13.5) - (22 x 13.5) =	50481 Persons
TOTAL		112991 Persons

POPULATION ACHIEVED IN GROUP HOUSING

S.NO.	GH AREA IN ACRES	PHASE	GROUP HOUSING POPULATION
1	14.75	I	4325
2	5.82	II	898
3	6.856	II	1036
4	6.46	II	1788
5	3.54	II	1227
6	9.458	III	1781
	TOTAL		11055

A	PLOTTED COLONY	112991
B	GROUP HOUSING	11,055
	TOTAL POPULATION	1,24,046

DETAILS OF INFRASTRUCTURE PROVIDED

SNO.	DESCRIPTION	PHASE-I PLOTTED	PHASE-I G.H.	PHASE-II PLOTTED	PHASE-II G.H.	PHASE-III PLOTTED	PHASE-III G.H.	TOTAL PLOTTED	TOTAL G.H.	TOTAL PROVIDED	TOTAL REQ.
1	CRECHE	04	0	03	0	05	0	12	0	12	08
2	NURSERY SCHOOL	15	02	12	0	21	0	48	02	50	50
3	PRIMARY SCHOOL	09	0	05	0	12	0	26	0	26	25
4	HIGH SCHOOL	[illegible]	[illegible]	[illegible]	[illegible]	[illegible]	[illegible]	[illegible]	[illegible]	[illegible]	[illegible]
5	CLUB/COMM. CENTRE	[illegible]	[illegible]	[illegible]	[illegible]	[illegible]	[illegible]	[illegible]	[illegible]	[illegible]	[illegible]
6	DISPENSARY	[illegible]	[illegible]	[illegible]	[illegible]	[illegible]	[illegible]	[illegible]	[illegible]	[illegible]	[illegible]
7	HEALTH CENTRE	[illegible]	[illegible]	[illegible]	[illegible]	[illegible]	[illegible]	[illegible]	[illegible]	[illegible]	[illegible]
8	RELIGIOUS BUILDING	[illegible]	[illegible]	[illegible]	[illegible]	[illegible]	[illegible]	[illegible]	[illegible]	[illegible]	[illegible]
9	ELECTRIC SUB STATION	[illegible]	[illegible]	[illegible]	[illegible]	[illegible]	[illegible]	[illegible]	[illegible]	[illegible]	[illegible]
10	TEL. FACILITY/EXCHANGE	[illegible]	[illegible]	[illegible]	[illegible]	[illegible]	[illegible]	[illegible]	[illegible]	[illegible]	[illegible]
11	POLICE POST	[illegible]	[illegible]	[illegible]	[illegible]	[illegible]	[illegible]	[illegible]	[illegible]	[illegible]	[illegible]
12	SUB POST OFFICE	[illegible]	[illegible]	[illegible]	[illegible]	[illegible]	[illegible]	[illegible]	[illegible]	[illegible]	[illegible]
	TOTAL	46	03	35	0	59	01	140	04	144	135

LEGEND:-

1. SCHEME BOUNDARY
2. UNLICENCED POCKETS SHOWN AS
3. INCIDENTAL GREENS/PARKS SHOWN AS
4. AREA WHERE PLANNING REVISED

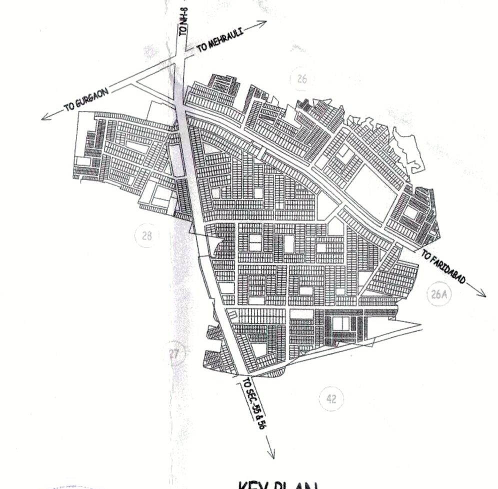

KEY PLAN

N

ARCHITECT/TOWN PLANNER

SCALE : 1:2500 | DATE : MAY, 2016 | DWG.NO. R-15

REVISED LAYOUT PLAN DLF CITY PHASE-I, GURGAON.