



Notes

1. Do not scale this drawing.
2. All dimensions must be checked on site and any discrepancies verified with the architect.
3. Unless shown otherwise, all dimensions are to structural surfaces.
4. Drawing to be read with all other issued information. Any discrepancies to be brought to the attention of the architect.
5. This drawing is the copyright of Levitt Bernstein and may not be copied, altered or reproduced in any form, or passed to a third party without license or written consent.
6. This document is prepared for the sole use of Haringey Council and no liability to any other persons is accepted by Levitt Bernstein. Levitt Bernstein accepts no liability for use of this drawing by parties other than the party for whom it was prepared or for purposes other than those for which it was prepared.

This is not a construction drawing, it is unsuitable for the purpose of construction and must on no account be used as such.



Note: All proposed drawings show emerging context. This includes Clarendon Gasworks Phase 5 proposed massing (as understood to be submitted as part of an RMA) and the buildings approved but yet to be completed: Chocolate Factory Phase 1 building E (HGY/2021/0624), Clarendon Gasworks Phase 4 (HGY/2023/2357).

P01	31.10.25	Planning Issue 01	MF
Rev	Date	Description	Drawn / Checked

Project name

Mallard Place
Stage 3

Drawing number	Rev
----------------	-----

4003A - LB - ZZ - 00 - D - A - 110000 **P01**

Drawing

Proposed Site Ground Plan

Purpose of issue	Date
Stage 3	31.10.25

Scale	Date
1 : 500 @ A1	31.10.25

Client	Haringey Council
--------	------------------

Levitt Bernstein
levittbernstein.co.uk

London
Thane Studios
2-4 Thane Villas
London N7 7PA
+44 (0)20 7275 7676
Manchester
Bonded Warehouse
18 Lower Byrom Street
Manchester M3 4AP
+44 (0)161 669 6740

1. Do not scale this drawing.
2. All dimensions must be checked on site and any discrepancies verified with the architect.
3. Unless shown otherwise, all dimensions are to structural surfaces.
4. Drawing to be read with all other issued information. Any discrepancies to be brought to the attention of the architect.
5. This drawing is the copyright of Levitt Bernstein and may not be copied, altered or reproduced in any form, or passed to a third party without license or written consent.
6. This document is prepared for the sole use of the Haverley Council.

It is the responsibility of any other persons is accepted by Levitt Bernstein. Levitt Bernstein accepts no liability for use of this drawing by parties other than the party for whom it was prepared or for purposes other than those for which it was prepared.

Note: All proposed drawings show emerging context. This includes Clarendon Gasworks Phase 5 proposed massing (as understood to be submitted as part of an RMA) and the buildings approved but yet to be completed: Chocolate Factory Phase 1 building E (HGY/2021/0624), Clarendon Gasworks Phase 4 (HGY/2023/2357).

BCW	Water & Water Meters
LANDLORD	Landlord Distribution Boards
MSDB	Multi Service Distribution Boards
COM	Telecoms, Access control & IRS
SP	Sprinklers
BUP	Backup LV
BUP GEN	Backup Generator Flue

WR	Wet Riser
DR	Dry Riser

SI	Smoke Shaft Intake
SE	Smoke Shaft Extract
AOV	Automatic Opening Vent (Stair Only)

4B&P Mais	Back Up Gen
Core Entrance	Heating Plant
Workspace	Inc Com
Flexible Commercial 01	Landlord LV Switch
Resi Bin Store	Life Safety LV Switch
Bulky Store	Substation
Comm Bin Store	Utility LV Switch
Comm cycle store	Water Services
Caretakers	Wet Riser Plant
Caretakers SL	

Crossrail tunnel indicated on GA plans to consulting Structural Engineers information and details

— Tunnel Centreline

— — — Exclusion Zone

P06	06.11.25	Planning Issue 02	MF
P05	31.10.25	Planning Issue 01	MF
P04	08.10.25	Draft Stage 3	MF
P03	05.09.25	Design Freeze Issue	MF
P02	25.07.25	Stage 2 Submission	MF
P01	20.06.25	Draft Stage 2	MF
Rev	Date	Description	Drawn / Checked

Project name

Stage 3

Drawing number Rev

4003A - LB - ZZ - 00 - D - A - 120100 P06

Drawing

GA Level 00 - Home Layouts

Purpose of issue

Stage 3

Scale Date
1 : 200 @ A1 20/06/25

Client
Haringey Council

London
Thane Studios
2-4 Thane Villas
London N7 7PA
+44 (0)20 7275 7676

Manchester
Bonded Warehouse
18 Lower Byrom Street
Manchester M3 4AP
+44 (0)161 669 8740

Levitt Bernstein
levittbernstein.co.uk

All additional fees are prepared for our client and are approximate only. They have been measured from the drawings available at the time and have been generated by Revit Model. We are not responsible for anomalies caused by plans generated by the Revit Model or those measured and calculated generally in accordance with RICS Code of Measuring Practice, 6th edition, 2007 and where Imperial units are given, they have been generated and converted from metric by the Revit Model. Measurements inherent in design documentation with IPMS 3B (RICS Property Measurement, 2nd edition, 2018) can be provided upon request for an additional fee. Areas are rounded to the nearest declared decimal Construction tolerances, workmanship and design by others may affect the stated areas. For existing buildings, the building may present anomalies in relation to surveyed/drawn plans that may also affect the stated areas. All these factors should be considered before making any decisions on the basis of these predictions, whether as to project viability, pre-letting, lease agreements or otherwise, and should include due allowance for the increases and decreases inherent in the design development and construction processes.

C:\Revit Local\4003A_Mallard Place-Building-R24-Central_hannah.williams8B99N.rvt

1. Do not scale this drawing.
2. All dimensions must be checked on site and any discrepancies verified with the architect.
3. Unless shown otherwise, all dimensions are to structural surfaces.
4. Drawing to be read with all other issued information. Any discrepancies to be brought to the attention of the architect.
5. This drawing is the copyright of Levitt Bernstein and may not be copied, altered or reproduced in any form, or passed to a third party without license or written consent.
6. This document is prepared for the sole use of the Housing Council and is not to be used by Levitt Bernstein. Levitt Bernstein accepts no liability for use of this drawing by parties other than the party for whom it was prepared or for purposes other than those for which it was prepared.

Note: All proposed drawings show emerging context. This includes Clarendon Gasworks Phase 5 proposed massing (as understood to be submitted as part of an RMA) and the buildings approved but yet to be completed: Chocolate Factory Phase 1 building E (HGY/2021/0624), Clarendon Gasworks Phase 4 (HGY/2023/2357).

BCW	Water & Water Meters
LANDLORD	Landlord Distribution Boards
MSDB	Multi Service Distribution Boards
COM	Telecoms, Access control & IRS
SP	Sprinklers
BUP	Backup LV
BUP GEN	Backup Generator Flue

ASHP Air Source Heat Pumps
HIU Heat Interface Units

WR Wet Riser
DR Dry Riser

SI	Smoke Shaft Intake
SE	Smoke Shaft Extract
AOV	Automatic Opening Vent (Stair Only)

1B2P	Accessible Bike Store
2B4P	Bike Store
4B8P Mails	Caretakers
Workspace	Comms
Workspace Breakout	Landlord LV Panel Board.

Crossrail tunnel indicated on GA plans to consulting Structural Engineers information and details

 Crossrail Tunnel
 Tunnel Centreline
 Exclusion Zone

P06	06.11.25	Planning Issue 02	MF
P05	31.10.25	Planning Issue 01	MF
P04	08.10.25	Draft Stage 3	MF
P03	05.09.25	Design Freeze Issue	MF
P02	25.07.25	Stage 2 Submission	MF
P01	20.06.25	Draft Stage 2	MF
Rev	Date	Description	Drawn / Checked

Project name

Drawing number Rev

4003A - LB - ZZ - 01 - D - A - 120101

Drawing

GA Level 01 - Home Layouts

Purpose of issue

Scale Date
1 : 200 @ A1 20/06/25

Client
Haringey Council

London
Thane Studios
2-4 Thane Villas
London N7 7PA
+44 (0)20 7275 7676

Manchester
Bonded Warehouse
18 Lower Byrom Street
Manchester M3 4AP
+44 (0)161 669 8740

Levitt Bernstein
levittbernstein.co.uk

These areas have been prepared for our client and are approximate only. They have been measured from the drawings available at the time and have been generated by the Revit Model. We are not responsible for anomalies caused by the Revit Model measured and calculated generally in accordance with theRICS Code of Measuring Practice, 6th edition, 2007 and have been calculated in metric units. Where imperial units are given, they have been generated and converted from metric by the Revit Model measured in accordance with IPMS 3B (RICS Property Measurement, 2nd edition, 2018) can be provided upon request for additional fees. Areas are rounded to the nearest declared decimal. Construction tolerances, workmanship and design by others may affect the stated areas. For existing buildings, the building may present anomalies in relation to surveyed/drawn plans that may affect the stated areas. All these factors should be considered before making any decisions on the basis of these predictions, whether as to project viability, pre-letting, lease agreements or otherwise, and should include due allowance for the increases and decreases inherent in the design development and construction processes.

C:\Revit Local\4003A_Mallard Place-Building-R24-Central_hannah.williams8B99N.rvt

1. Do not scale this drawing.
2. All dimensions must be checked on site and any discrepancies verified with the architect.
3. Unless shown otherwise, all dimensions are to structural surfaces.
4. Drawing to be read with all other issued information. Any discrepancies to be brought to the attention of the architect.
5. This drawing is the copyright of Levitt Bernstein and may not be copied, altered or reproduced in any form, or passed to a third party without license or written consent.
6. This document is prepared for the sole use of Harington Council and is not to be lent to any other persons is accepted by Levitt Bernstein. Levitt Bernstein accepts no liability for use of this drawing by parties other than the party for whom it was prepared or for purposes other than those for which it was prepared.

Note: All proposed drawings show emerging context. This includes Clarendon Gasworks Phase 5 proposed massing (as understood to be submitted as part of an RMA) and the buildings approved but yet to be completed: Chocolate Factory Phase 1 building E (HGY/2021/0624), Clarendon Gasworks Phase 4 (HGY/2023/2357).

BCW	Water & Water Meters
LANDLORD	Landlord Distribution Boards
MSDB	Multi Service Distribution Boards
COM	Telecoms, Access control & IRS
SP	Sprinklers
BUP	Backup LV
BUP GEN	Backup Generator Flue

WR Wet Rise
DR Dry Riser

Room Name

 1B2P	 3B4P
 2B3P	 3B4P WCH
 2B3P WCH	 4B8P Mais
 2B4P	 Caretakers

Crossrail tunnel indicated on GA plans to consulting Structural Engineers information and details

- Crossrail Tunnel
 Tunnel Centreline
 Exclusion Zone

P06	06.11.25	Planning Issue 02	MF
P05	31.10.25	Planning Issue 01	MF
P04	08.10.25	Draft Stage 3	MF
P03	05.09.25	Design Freeze Issue	MF
P02	25.07.25	Stage 2 Submission	MF
P01	20.06.25	Draft Stage 2	MF
Rev	Date	Description	Drawn / Checked

Project name

Drawing number Rev

4003A - LB - ZZ - 02 - D - A - 120102 P06

Drawing

Purpose of issue

Scale	Date
1 : 200 @ A1	20/06/25

Client
Haringey Council

London
Thane Studios
2-4 Thane Villas
London N7 7PA
+44 (0)20 7275 7676

Manchester
Bonded Warehouse
18 Lower Byrom Street
Manchester M3 4AP
+44 (0)161 669 8740

Levitt Bernstein
levittbernstein.co.uk

Additional fees are prepared for our client and are approximate only. They have been measured from the drawings available at the time and have been generated for the Revit Model. We are not responsible for anomalies caused by areas generated by the Revit software measured and calculated generally in accordance with RICS Code of Measuring Practice, 6th edition, 2007 and 2018, where imperial units are given, they have been generated and converted from metric by the Revit Model. Measures measured in accordance with IPMS 3b (RICS Property Measurement, 2nd edition, 2018) can be provided upon request for areas above the floor level. Additional fees are prepared for the nearest declared decimal/Construction tolerances, workmanship and design by others may affect the stated areas. For existing buildings, the building may present anomalies in relation to surveyed/drawn plans that may also affect the stated areas. All these factors should be considered before making any decisions on the basis of these predictions, whether as to project viability, pre-letting, lease agreements or otherwise, and should include due allowance for the increases and decreases inherent in the design development and construction process.

C:\Revit Local\4003A_Mallard Place-Building-R24-Central_hannah.williams8B99N.rvt

1. Do not scale this drawing.
2. All dimensions must be checked on site and any discrepancies verified with the architect.
3. Unless shown otherwise, all dimensions are to structural surfaces.
4. Drawing to be read with all other issued information. Any discrepancies to be brought to the attention of the architect.
5. This drawing is the copyright of Levitt Bernstein and may not be copied, altered or reproduced in any form, or passed to a third party without license or written consent.
6. This document is prepared for the sole use of the Houghton Council and is not to be used by Levitt Bernstein. Levitt Bernstein accepts no liability for use of this drawing by parties other than the party for whom it was prepared or for purposes other than those for which it was prepared.

Riser Types

BCW	Water & Water Meters
LANDLORD	Landlord Distribution Boards
MSDB	Multi Service Distribution Boards
COM	Telecoms, Access control & IRS
SP	Sprinklers
BU1P	Backup LV
BU1P GEN	Backup Generator Flue
ASHP	Air Source Heat Pumps
HIU	Heat Interface Units
WR	Wet Riser
DR	Dry Riser
SI	Smoke Shaft Intake
SE	Smoke Shaft Extract
AOV	Automatic Opening Vent (Stair Only)

1B2P	3B4P
2B3P	3B4P WCH
2B3P WCH	3B5P
2B4P	

Crossrail tunnel indicated on GA plans to consulting Structural Engineers information and details

- — — Crossrail Tunnel
- Tunnel Centreline
- — — Exclusion Zone

P06	06.11.25	Planning Issue 02	MF
P05	31.10.25	Planning Issue 01	MF
P04	08.10.25	Draft Stage 3	MF
P03	05.09.25	Design Freeze Issue	MF
P02	25.07.25	Stage 2 Submission	MF
P01	20.06.25	Draft Stage 2	MF
Rev	Date	Description	Drawn / Checked

Project name

Drawing number _____ Rev _____

4003A - LB - ZZ - 03 - D - A - 120103 **P06**

Stage 3

Scale Date
1 : 200 @ A1 20/06/25

Client
Haringey Council

London
Thane Studios
2-4 Thane Villas
London N7 7PA
+44 (0)20 7275 7676

Manchester
Bonded Warehouse
18 Lower Byrom Street
Manchester M3 4AP
+44 (0)161 669 8740

Levitt Bernstein
levittbernstein.co.uk



Notes

1. Do not scale this drawing.
2. All dimensions must be checked on site and any discrepancies verified with the architect.
3. Unless shown otherwise, all dimensions are to structural surfaces.
4. Drawing to be read with all other issued information. Any discrepancies to be brought to the attention of the architect.
5. This drawing is the copyright of Levitt Bernstein and may not be copied, altered or reproduced in any form, or passed to a third party without license or written consent.
6. This document is prepared for the sole use of Haringey Council and no liability to any other persons is accepted by Levitt Bernstein. Levitt Bernstein accepts no liability for use of this drawing by parties other than the party for whom it was prepared or for purposes other than those for which it was prepared.

This is not a construction drawing, it is unsuitable for the purpose of construction and must on no account be used as such.

Note: All proposed drawings show emerging context. This includes Clarendon Gasworks Phase 5 proposed massing (as understood to be submitted as part of an RMA) and the buildings approved but yet to be completed: Chocolate Factory Phase 1 building E (HGY/2021/0624), Clarendon Gasworks Phase 4 (HGY/2023/2357).

Riser Types

BCW	Water & Water Meters
LANDLORD	Landlord Distribution Boards
MSDB	Multi Service Distribution Boards
COM	Telecoms, Access control & IRS
SP	Sprinklers
BUP	Backup LV
BUP GEN	Backup Generator Flue
ASHP	Air Source Heat Pumps
HIU	Heat Interface Units
WR	Wet Riser
DR	Dry Riser
SI	Smoke Shaft Intake
SE	Smoke Shaft Extract
AOV	Automatic Opening Vent (Stair Only)

Room Name

1B2P	3B4P
2B3P	3B4P WCH
2B3P WCH	3B5P
2B4P	

Crossrail Tunnel Key

Crossrail tunnel indicated on GA plans to consulting Structural Engineers information and details

—	Crossrail Tunnel
—	Tunnel Centreline
---	Exclusion Zone

P04	06.11.25	Planning Issue 02	MF
P03	31.10.25	Planning Issue 01	MF
P02	08.10.25	Draft Stage 3	MF
P01	05.09.25	Design Freeze Issue	MF
Rev	Date	Description	Drawn / Checked

Project name

Mallard Place Stage 3

Drawing number Rev

4003A - LB - ZZ - 04 - D - A - 120104 **P04**

Drawing

GA Level 04 - Home Layouts

Purpose of issue

Stage 3

Scale Date
1 : 200 @ A1 20/12/24

Client
Haringey Council

London
Thane Studios
2-4 Thane Villas
London N7 7PA
+44 (0)20 7275 7676
Manchester
Bonded Warehouse
18 Lower Byron Street
Manchester M3 4AP
+44 (0)161 669 6740

Levitt Bernstein
levittbernstein.co.uk

1. Do not scale this drawing.
2. All dimensions must be checked on site and any discrepancies verified with the architect.
3. Unless shown otherwise, all dimensions are to structural surfaces.
4. Drawing to be read with all other issued information. Any discrepancies to be brought to the attention of the architect.
5. This drawing is the copyright of Levitt Bernstein and may not be copied, altered or reproduced in any form, or passed to a third party without license or written consent.
6. This document is prepared for the sole use of the Planning, Design and Construction Committee and is not to be used by any other persons is accepted by Levitt Bernstein. Levitt Bernstein accepts no liability for use of this drawing by parties other than the party for whom it was prepared or for purposes other than those for which it was prepared.

This is not a construction drawing, it is unsuitable for the purpose of construction and must on no account be used as such.

Note: All proposed drawings show emerging context. This includes Clarendon Gasworks Phase 5 proposed massing (as understood to be submitted as part of an RMA) and the buildings approved but yet to be completed: Chocolate Factory Phase 1 building E (HGY/2021/0624), Clarendon Gasworks Phase 4 (HGY/2023/2357).

BCW	Water & Water Meters
LANDLORD	Landlord Distribution Boards
MSDB	Multi Service Distribution Boards
COM	Telecoms, Access control & IRS
SP	Sprinklers
BUP	Backup LV
BUP GEN	Backup Generator Flue
ASHP	Air Source Heat Pumps
HIU	Heat Interface Units
WR	Wet Riser
DR	Dry Riser
SI	Smoke Shaft Intake
SE	Smoke Shaft Extract
AOV	Automatic Opening Vent (Stair Only)

	1B2P		3B4P
	2B3P		3B4P WCH
	2B3P WCH		3B5P
	2B4P		

Crossrail tunnel indicated on GA plans to consulting Structural Engineers information and details

- Crossrail Tunnel
— Tunnel Centreline
--- Exclusion Zone

P03	06.11.25	Planning Issue 02	MF
P02	31.10.25	Planning Issue 01	MF
P01	08.10.25	Draft Stage 3	MF
Rev	Date	Description	Drawn / Checked

Project name

Drawing number Rev

4003A - LB - ZZ - 05 - D - A - 120105 P03

Drawing

Stage 3

Scale	Date
1 : 200 @ A1	08.10.25

Client
Haringey Council

London
Thane Studios
2-4 Thane Villas
London N7 7PA
+44 (0)20 7275 7876

Manchester
Bonded Warehouse
18 Lower Byron Street
Manchester M3 4AP
+44 (0)161 669 8740

Levitt Bernstein
levittbernstein.co.uk

These areas have been prepared for our client and are approximate only. They have been measured from the drawings available at the time and have been generated by the Revit Model. We are not responsible for anomalies caused by areas generated by the Revit Model. Measurements are measured and calculated generally in accordance with RICS Code of Measuring Practice, 8th edition, 2007 and 2018, where Imperial units are given, they have been generated and converted from metric by the Revit Model. Measurements measured in accordance with IPMS 3B (RICS Property Measurement, 2nd edition, 2018) can be provided upon request for additional fee. Areas are rounded to the nearest declared decimal/Construction Tolerances, workmanship and design by others may affect the stated areas. For existing buildings, the building may present anomalies in relation to surveyed/drawn plans that may also affect the stated areas. All these factors should be considered before making any decisions on the basis of these predictions, whether as to project viability, pre-letting, lease agreements or otherwise, and should include due allowance for the increases and decreases inherent in the design development and construction processes.

C:\Revit Local\4003A_Mallard Place-Building-R24-Central_hannah.williams8B99N.rvt

1. Do not scale this drawing.
2. All dimensions must be checked on site and any discrepancies verified with the architect.
3. Unless shown otherwise, all dimensions are to structural surfaces.
4. Drawing to be read with all other issued information. Any discrepancies to be brought to the attention of the architect.
5. This drawing is the copyright of Levitt Bernstein and may not be copied, altered or reproduced in any form, or passed to a third party without license or written consent.
6. This document is prepared for the sole use of the Haverly Council.
7. No liability to any other persons is accepted by Levitt Bernstein. Levitt Bernstein accepts no liability for use of this drawing by parties other than the party for whom it was prepared or for purposes other than those for which it was prepared.

This is not a construction drawing, it is unsuitable for the purpose of construction and must on no account be used as such.

Note: All proposed drawings show emerging context. This includes Clarendon Gasworks Phase 5 proposed massing (as understood to be submitted as part of an RMA) and the buildings approved but yet to be completed: Chocolate Factory Phase 1 building E (HGY/2021/0624), Clarendon Gasworks Phase 4 (HGY/2023/2357).

BCW	Water & Water Meters
LANDLORD	Landlord Distribution Boards
MSDB	Multi Service Distribution Boards
COM	Telecoms, Access control & IRS
SP	Sprinklers
BUF	Backup LV
BUF GEN	Backup Generator Flue
ASHP	Air Source Heat Pumps
HIU	Heat Interface Units
WR	Wet Riser
DR	Dry Riser
SI	Smoke Shaft Intake
SE	Smoke Shaft Extract
AOV	Automatic Opening Vent (Stair Only)

	1B2P		3B4P
	2B3P		3B4P WCH
	2B3P WCH		3B5P
	2B4P		Caretakers

Crossrail tunnel indicated on GA plans to consulting Structural Engineers information and details

- Crossrail Tunnel
— Tunnel Centreline
--- Exclusion Zone

P06	06.11.25	Planning Issue 02	MF
P05	31.10.25	Planning Issue 01	MF
P04	08.10.25	Draft Stage 3	MF
P03	05.09.25	Design Freeze Issue	MF
P02	25.07.25	Stage 2 Submission	MF
P01	20.06.25	Draft Stage 2	MF
Rev	Date	Description	Drawn / Checked

Project name

Drawing number Rev

4003A - LB - ZZ - 06 - D - A - 120106 P06

Drawing

Purpose of issue

Scale Date
1 : 200 @ A1 20/06/25

Client
Haringey Council

London
Thane Studios
2-4 Thane Villas
London N7 7PA
+44 (0)20 7275 7676

Manchester
Bonded Warehouse
18 Lower Byrom Street
Manchester M3 4AP
+44 (0)161 669 8740

Levitt Bernstein
levittbernstein.co.uk

C:\Rwdt Local\4003A_Mallard Place-Building-B24-Central_hannah.williams8B99N



- Notes**
1. Do not scale this drawing.
 2. All dimensions must be checked on site and any discrepancies verified with the architect.
 3. Unless shown otherwise, all dimensions are to structural surfaces.
 4. Drawing to be read with all other issued information. Any discrepancies to be brought to the attention of the architect.
 5. This drawing is the copyright of Levitt Bernstein and may not be copied, altered or reproduced in any form, or passed to a third party without license or written consent.
 6. This document is prepared for the sole use of Haringey Council and no liability to any other persons is accepted by Levitt Bernstein. Levitt Bernstein accepts no liability for use of this drawing by parties other than the party for whom it was prepared or for purposes other than those for which it was prepared.

This is not a construction drawing, it is unsuitable for the purpose of construction and must on no account be used as such.

Note: All proposed drawings show emerging context. This includes Clarendon Gasworks Phase 5 proposed massing (as understood to be submitted as part of an RMA) and the buildings approved but yet to be completed: Chocolate Factory Phase 1 building E (HGY/2021/0624), Clarendon Gasworks Phase 4 (HGY/2023/2357).

Riser Types

BCW	Water & Water Meters
LANDLORD	Landlord Distribution Boards
MSDB	Multi Service Distribution Boards
COM	Telecoms, Access control & IRS
SP	Sprinklers
BUP	Backup LV
BUP GEN	Backup Generator Flue
ASHP	Air Source Heat Pumps
HIU	Heat Interface Units
WR	Wet Riser
DR	Dry Riser
SI	Smoke Shaft Intake
SE	Smoke Shaft Extract
AOV	Automatic Opening Vent (Stair Only)

Room Name

1B2P	2B4P
2B3P	3B4P
2B3P WCH	3B4P WCH

Crossrail Tunnel Key

Crossrail tunnel indicated on GA plans to consulting Structural Engineers information and details

—	Crossrail Tunnel
—	Tunnel Centreline
---	Exclusion Zone

P06	06.11.25	Planning Issue 02	MF
P05	31.10.25	Planning Issue 01	MF
P04	08.10.25	Draft Stage 3	MF
P03	05.09.25	Design Freeze Issue	MF
P02	25.07.25	Stage 2 Submission	MF
P01	20.06.25	Draft Stage 2	MF
Rev	Date	Description	Drawn / Checked

Project name

Mallard Place
Stage 3

Drawing number Rev

4003A - LB - ZZ - 07 - D - A - 120107 **P06**

Drawing

GA Level 07 - Home Layouts

Purpose of issue
Stage 3

Scale Date
1 : 200 @ A1 20/06/25

Client
Haringey Council

London
Thane Studios
2-4 Thane Villas
London N7 7PA
+44 (0)20 7275 7676
Manchester
Bonded Warehouse
18 Lower Byron Street
Manchester M3 4AP
+44 (0)161 669 6740

Levitt Bernstein
levittbernstein.co.uk



Notes

1. Do not scale this drawing.
2. All dimensions must be checked on site and any discrepancies verified with the architect.
3. Unless shown otherwise, all dimensions are to structural surfaces.
4. Drawing to be read with all other issued information. Any discrepancies to be brought to the attention of the architect.
5. This drawing is the copyright of Levitt Bernstein and may not be copied, altered or reproduced in any form, or passed to a third party without license or written consent.
6. This document is prepared for the sole use of Haringey Council and no liability to any other persons is accepted by Levitt Bernstein. Levitt Bernstein accepts no liability for use of this drawing by parties other than the party for whom it was prepared or for purposes other than those for which it was prepared.

This is not a construction drawing, it is unsuitable for the purpose of construction and must on no account be used as such.

Note: All proposed drawings show emerging context. This includes Clarendon Gasworks Phase 5 proposed massing (as understood to be submitted as part of an RMA) and the buildings approved but yet to be completed: Chocolate Factory Phase 1 building E (HGY/2021/0624), Clarendon Gasworks Phase 4 (HGY/2023/2357).

Riser Types

BCW	Water & Water Meters
LANDLORD	Landlord Distribution Boards
MSDB	Multi Service Distribution Boards
COM	Telecoms, Access control & IRS
SP	Sprinklers
BUP	Backup LV
BUP GEN	Backup Generator Flue
ASHP	Air Source Heat Pumps
HIU	Heat Interface Units
WR	Wet Riser
DR	Dry Riser
SI	Smoke Shaft Intake
SE	Smoke Shaft Extract
AOV	Automatic Opening Vent (Stair Only)

Room Name

1B2P	Caretakers
2B3P	
2B4P	
3B5P	

Crossrail Tunnel Key

Crossrail tunnel indicated on GA plans to consulting Structural Engineers information and details

—	Crossrail Tunnel
—	Tunnel Centreline
---	Exclusion Zone

P05	06.11.25	Planning Issue 02	MF
P04	31.10.25	Planning Issue 01	MF
P03	08.10.25	Draft Stage 3	MF
P02	05.09.25	Design Freeze Issue	MF
P01	20.06.25	Draft Stage 2	MF
Rev	Date	Description	Drawn / Checked

Project name

Mallard Place Stage 3

Drawing number Rev

4003A - LB - ZZ - 08 - D - A - 120108 **P05**

Drawing

GA Level 08 - Home Layouts

Purpose of issue

Stage 3

Scale Date
1 : 200 @ A1 20/06/25

Client
Haringey Council

London
Thane Studios
2-4 Thane Villas
London N1 7PA
+44 (0)20 7275 7676
Manchester
Bonded Warehouse
18 Lower Byrom Street
Manchester M3 4AP
+44 (0)161 669 6740

Levitt Bernstein
levittbernstein.co.uk



Notes

1. Do not scale this drawing.
2. All dimensions must be checked on site and any discrepancies verified with the architect.
3. Unless shown otherwise, all dimensions are to structural surfaces.
4. Drawing to be read with all other issued information. Any discrepancies to be brought to the attention of the architect.
5. This drawing is the copyright of Levitt Bernstein and may not be copied, altered or reproduced in any form, or passed to a third party without license or written consent.
6. This document is prepared for the sole use of Haringey Council and no liability to any other persons is accepted by Levitt Bernstein. Levitt Bernstein accepts no liability for use of this drawing by parties other than the party for whom it was prepared or for purposes other than those for which it was prepared.

This is not a construction drawing, it is unsuitable for the purpose of construction and must on no account be used as such.

Note: All proposed drawings show emerging context. This includes Clarendon Gasworks Phase 5 proposed massing (as understood to be submitted as part of an RMA) and the buildings approved but yet to be completed: Chocolate Factory Phase 1 building E (HGY/2021/0624), Clarendon Gasworks Phase 4 (HGY/2023/2357).

Riser Types

BCW	Water & Water Meters
LANDLORD	Landlord Distribution Boards
MSDB	Multi Service Distribution Boards
COM	Telecoms, Access control & IRS
SP	Sprinklers
BUP	Backup LV
BUP GEN	Backup Generator Flue
ASHP	Air Source Heat Pumps
HIU	Heat Interface Units
WR	Wet Riser
DR	Dry Riser
SI	Smoke Shaft Intake
SE	Smoke Shaft Extract
AOV	Automatic Opening Vent (Stair Only)

Room Name

1B2P
2B3P
2B4P

Crossrail Tunnel Key

Crossrail tunnel indicated on GA plans to consulting Structural Engineers information and details

---	Crossrail Tunnel
---	Tunnel Centreline
---	Exclusion Zone

P06	06.11.25	Planning Issue 02	MF
P05	31.10.25	Planning Issue 01	MF
P04	08.10.25	Draft Stage 3	MF
P03	05.09.25	Design Freeze Issue	MF
P02	25.07.25	Stage 2 Submission	MF
P01	20.06.25	Draft Stage 2	MF
Rev	Date	Description	Drawn / Checked

Project name

Mallard Place
Stage 3

Drawing number Rev

4003A - LB - ZZ - 09 - D - A - 120109 P06

Drawing

GA Level 09 - Home Layouts

Stage 3

Scale Date
1 : 200 @ A1 20/06/25

Client
Haringey Council

Levitt Bernstein
levittbernstein.co.uk

London
Thane Studios
2-4 Thane Villas
London N7 7PA
+44 (0)20 7275 7676
Manchester
Bonded Warehouse
18 Lower Byron Street
Manchester M3 4AP
+44 (0)161 669 6740

1. Do not scale this drawing.
2. All dimensions must be checked on site and any discrepancies verified with the architect.
3. Unless shown otherwise, all dimensions are to structural surfaces.
4. Drawing to be read with all other issued information. Any discrepancies to be brought to the attention of the architect.
5. This drawing is the copyright of Levitt Bernstein and may not be copied, altered or reproduced in any form, or passed to a third party without license or written consent.
6. This document is prepared for the sole use of
Haringey Council
and may not be used by any other persons is accepted by Levitt Bernstein. Levitt Bernstein accepts no liability for use of this drawing by parties other than the party for whom it was prepared or for purposes other than those for which it was prepared.

Note: All proposed drawings show emerging context. This includes Clarendon Gasworks Phase 5 proposed massing (as understood to be submitted as part of an RMA) and the buildings approved but yet to be completed: Chocolate Factory Phase 1 building E (HGY/2021/0624), Clarendon Gasworks Phase 4 (HGY/2023/2357).

BCW	Water & Water Meters
LANDLORD	Landlord Distribution Boards
MSDB	Multi Service Distribution Boards
COM	Telecoms, Access control & IRS
SP	Sprinklers
BUP	Backup LV
BUP GEN	Backup Generator Flue

WR Wet Rise
DR Dry Riser

Room Name

08.15

Crossrail tunnel indicated on GA plans to consulting Structural Engineers information and details

— — — Exclusion Zone

Project name

Stage 3

Drawing number _____ Rev _____

Drawing

GA Level 10 - Home Layouts

Purpose of issue

Scale Date
1 : 200 @ A1 08.10.25

Client
Haringey Council

London
Thane Studios
2-4 Thane Villas
London N7 7PA
+44 (0)20 7275 7676

Manchester
Bonded Warehouse
18 Lower Byrom Street
Manchester M3 4AP
+44 (0)161 669 8740

Levitt Bernstein
levittbernstein.co.uk

Levitt Bernstein
levittbernstein.co.uk

London
Thane Studios
2-4 Thane Villas
London N7 7PA
+44 (0)20 7275 7676

Manchester
Bonded Warehouse
18 Lower Byrom Street
Manchester M3 4AP
+44 (0)161 669 8740

These areas have been prepared for our client and are approximate only. They have been measured from the drawings available at the time and have been generated by the Revit Model. We are not responsible for anomalies caused by areas generated by the Revit Model. Measurements are measured and calculated generally in accordance with RICS Code of Measuring Practice, 8th edition, 2007 and 2018. Where Imperial units are given, they have been generated and converted from metric by the Revit Model. Measurements measured in accordance with IPMS 3B (RICS Property Measurement, 2nd edition, 2018) can be provided upon request for additional fee. Areas are rounded to the nearest declared decimal. Construction tolerances, workmanship and design by others may affect the stated areas. For existing buildings, the building may present anomalies in relation to surveyed/drawn plans that may also affect the stated areas. All these factors should be considered before making any decisions on the basis of these predictions, whether as to project viability, pre-letting, lease agreements or otherwise, and should include due allowance for the increases and decreases inherent in the design development and construction processes.

C:\Revit Local\4003A_Mallard Place-Building-R24-Central_hannah.williams8B99N.rvt

1. Do not scale this drawing.
2. All dimensions must be checked on site and any discrepancies verified with the architect.
3. Unless shown otherwise, all dimensions are to structural surfaces.
4. Drawing to be read with all other issued information. Any discrepancies to be brought to the attention of the architect.
5. This drawing is the copyright of Levitt Bernstein and may not be copied, altered or reproduced in any form, or passed to a third party without license or written consent.
6. This document is prepared for the sole use of
Haringey Council
and may not be used by any other persons is accepted by Levitt Bernstein. Levitt Bernstein accepts no liability for use of this drawing by parties other than the party for whom it was prepared or for purposes other than those for which it was prepared.

Note: All proposed drawings show emerging context. This includes Clarendon Gasworks Phase 5 proposed massing (as understood to be submitted as part of an RMA) and the buildings approved but yet to be completed: Chocolate Factory Phase 1 building E (HGY/2021/0624), Clarendon Gasworks Phase 4 (HGY/2023/2357).

BCW	Water & Water Meters
LANDLORD	Landlord Distribution Boards
MSDB	Multi Service Distribution Boards
COM	Telecoms, Access control & IRS
SP	Sprinklers
BUP	Backup LV
BUP GEN	Backup Generator Flue

WR Wet Riser
DR Dry Riser

Room Name

Crossrail tunnel indicated on GA plans to consulting Structural Engineers information and details

- — — Crossrail Tunnel
- Tunnel Centreline
- — — Exclusion Zone

P03	06.11.25	Planning Issue 02	MF
P02	31.10.25	Planning Issue 01	MF
P01	08.10.25	Draft Stage 3	MF
Rev	Date	Description	Drawn / Checked

Project name

Stage 3

Drawing number Rev

Drawing

Purpose of

Scale Date
1 : 200 @ A1 08.10.25

Client
Haringey Council

London
Thane Studios
2-4 Thane Villas
London N7 7PA
+44 (0)20 7275 7676

Manchester
Bonded Warehouse
18 Lower Byrom Street
Manchester M3 4AP
+44 (0)161 669 8740

Levitt Bernstein
levittbernstein.co.uk

Additional fees are prepared for our client and are approximate only. They have been measured from the drawings available at the time and have been generated by the Revit Model. We are not responsible for anomalies caused by areas generated by the Revit Model. **Measurements** measured and calculated generally in accordance with RICS Code of Measuring Practice, 6th edition, 2007, and those that have been calculated in pre-titles. Where imperial units are given, they have been generated and converted from metric by the Revit Model. **Measures** inherent in design and construction with IPMS 3B (RICS Property Measurement, 2nd edition, 2018) can be provided upon request for any additional fees. Areas are rounded to the nearest declared decimal. Construction tolerances, workmanship and design by others may affect the stated areas. For existing buildings, the building may present anomalies in relation to surveyed/drawn plans that may also affect the measured areas. All these factors should be considered before making any decisions on the basis of these predictions, whether as to project viability, pre-letting, lease agreements or otherwise, and should include due allowance for the increases and decreases inherent in the design development and construction process.

C:\Revit Local\4003A_Mallard Place-Building-R24-Central_hannah.williams8B99N.rvt

1. Do not scale this drawing.
2. All dimensions must be checked on site and any discrepancies verified with the architect.
3. Unless shown otherwise, all dimensions are to structural surfaces.
4. Drawing to be read with all other issued information. Any discrepancies to be brought to the attention of the architect.
5. This drawing is the copyright of Levitt Bernstein and may not be copied, altered or reproduced in any form, or passed to a third party without license or written consent.
6. This document is prepared for the sole use of the Housing Council and is not to be used by Levitt Bernstein. Levitt Bernstein accepts no liability for use of this drawing by parties other than the party for whom it was prepared or for purposes other than those for which it was prepared.

This is not a construction drawing, it is unsuitable for the purpose of construction and must on no account be used as such.



Note: All proposed drawings show emerging context. This includes Clarendon Gasworks Phase 5 proposed massing (as understood to be submitted as part of an RMA) and the buildings approved but yet to be completed: Chocolate Factory Phase 1 building E (HGY/2021/0624), Clarendon Gasworks Phase 4 (HGY/2023/2357).

BCW

BCW	Water & Water Meters
LANDLORD	Landlord Distribution Boards
MSDB	Multi Service Distribution Boards
COM	Telecoms, Access control & IRS
SP	Sprinklers
BUP	Backup LV
BUP GEN	Backup Generator Flue
ASHP	Air Source Heat Pumps
HIU	Heat Interface Units
WR	Wet Riser
DR	Dry Riser
SI	Smoke Shaft Intake
SE	Smoke Shaft Extract
AOV	Automatic Opening Vent (Stair Only)

1B2P
2B3P
2B4P

Crossrail tunnel indicated on GA plans to consulting Structural Engineers information and details

- — — Crossrail Tunnel
- Tunnel Centreline
- — — Exclusion Zone

P03	06.11.25	Planning Issue 02	MF
P02	31.10.25	Planning Issue 01	MF
P01	08.10.25	Draft Stage 3	MF
Rev	Date	Description	Drawn / Checked

Project name

Drawing number Rev

4003A - LB - ZZ - 12 - D - A - 120112 P03

Drawing

Purpose of issue

Stage 3

Scale	Date
1 : 200 @ A1	08.10.25


Client
Haringey Council

London
Thane Studios
2-4 Thane Villas
London N7 7PA
+44 (0)20 7275 7676

Manchester
Bonded Warehouse
18 Lower Byrom Street
Manchester M3 4AP
+44 (0)161 669 8740

Levitt Bernstein
levittbernstein.co.uk

Additional fees are prepared for our client and are approximate only. They have been measured from the drawings available at the time and have been generated by the Revit Model. We are not responsible for anomalies caused by areas generated by the Revit Model. Measurements are measured and calculated generally in accordance with RICS Code of Measuring Practice, 6th edition, 2007 and 2018. Where imperial units are given, they have been generated and converted from metric by the Revit Model. Measurements are measured in accordance with IPMS 3B (RICS Property Measurement, 2nd edition, 2018) can be provided upon request for the above areas. Areas are rounded to the nearest declared decimal/Construction tolerances, workmanship and design by which they affect the stated areas. For existing buildings, the building may present anomalies in relation to surveyed/drawn plans that may also affect the stated areas. All these factors should be considered before making any decisions on the basis of these predictions, whether as to project viability, pre-letting, lease agreements or otherwise, and should include due allowance for the increases and decreases inherent in the design development and construction processes.

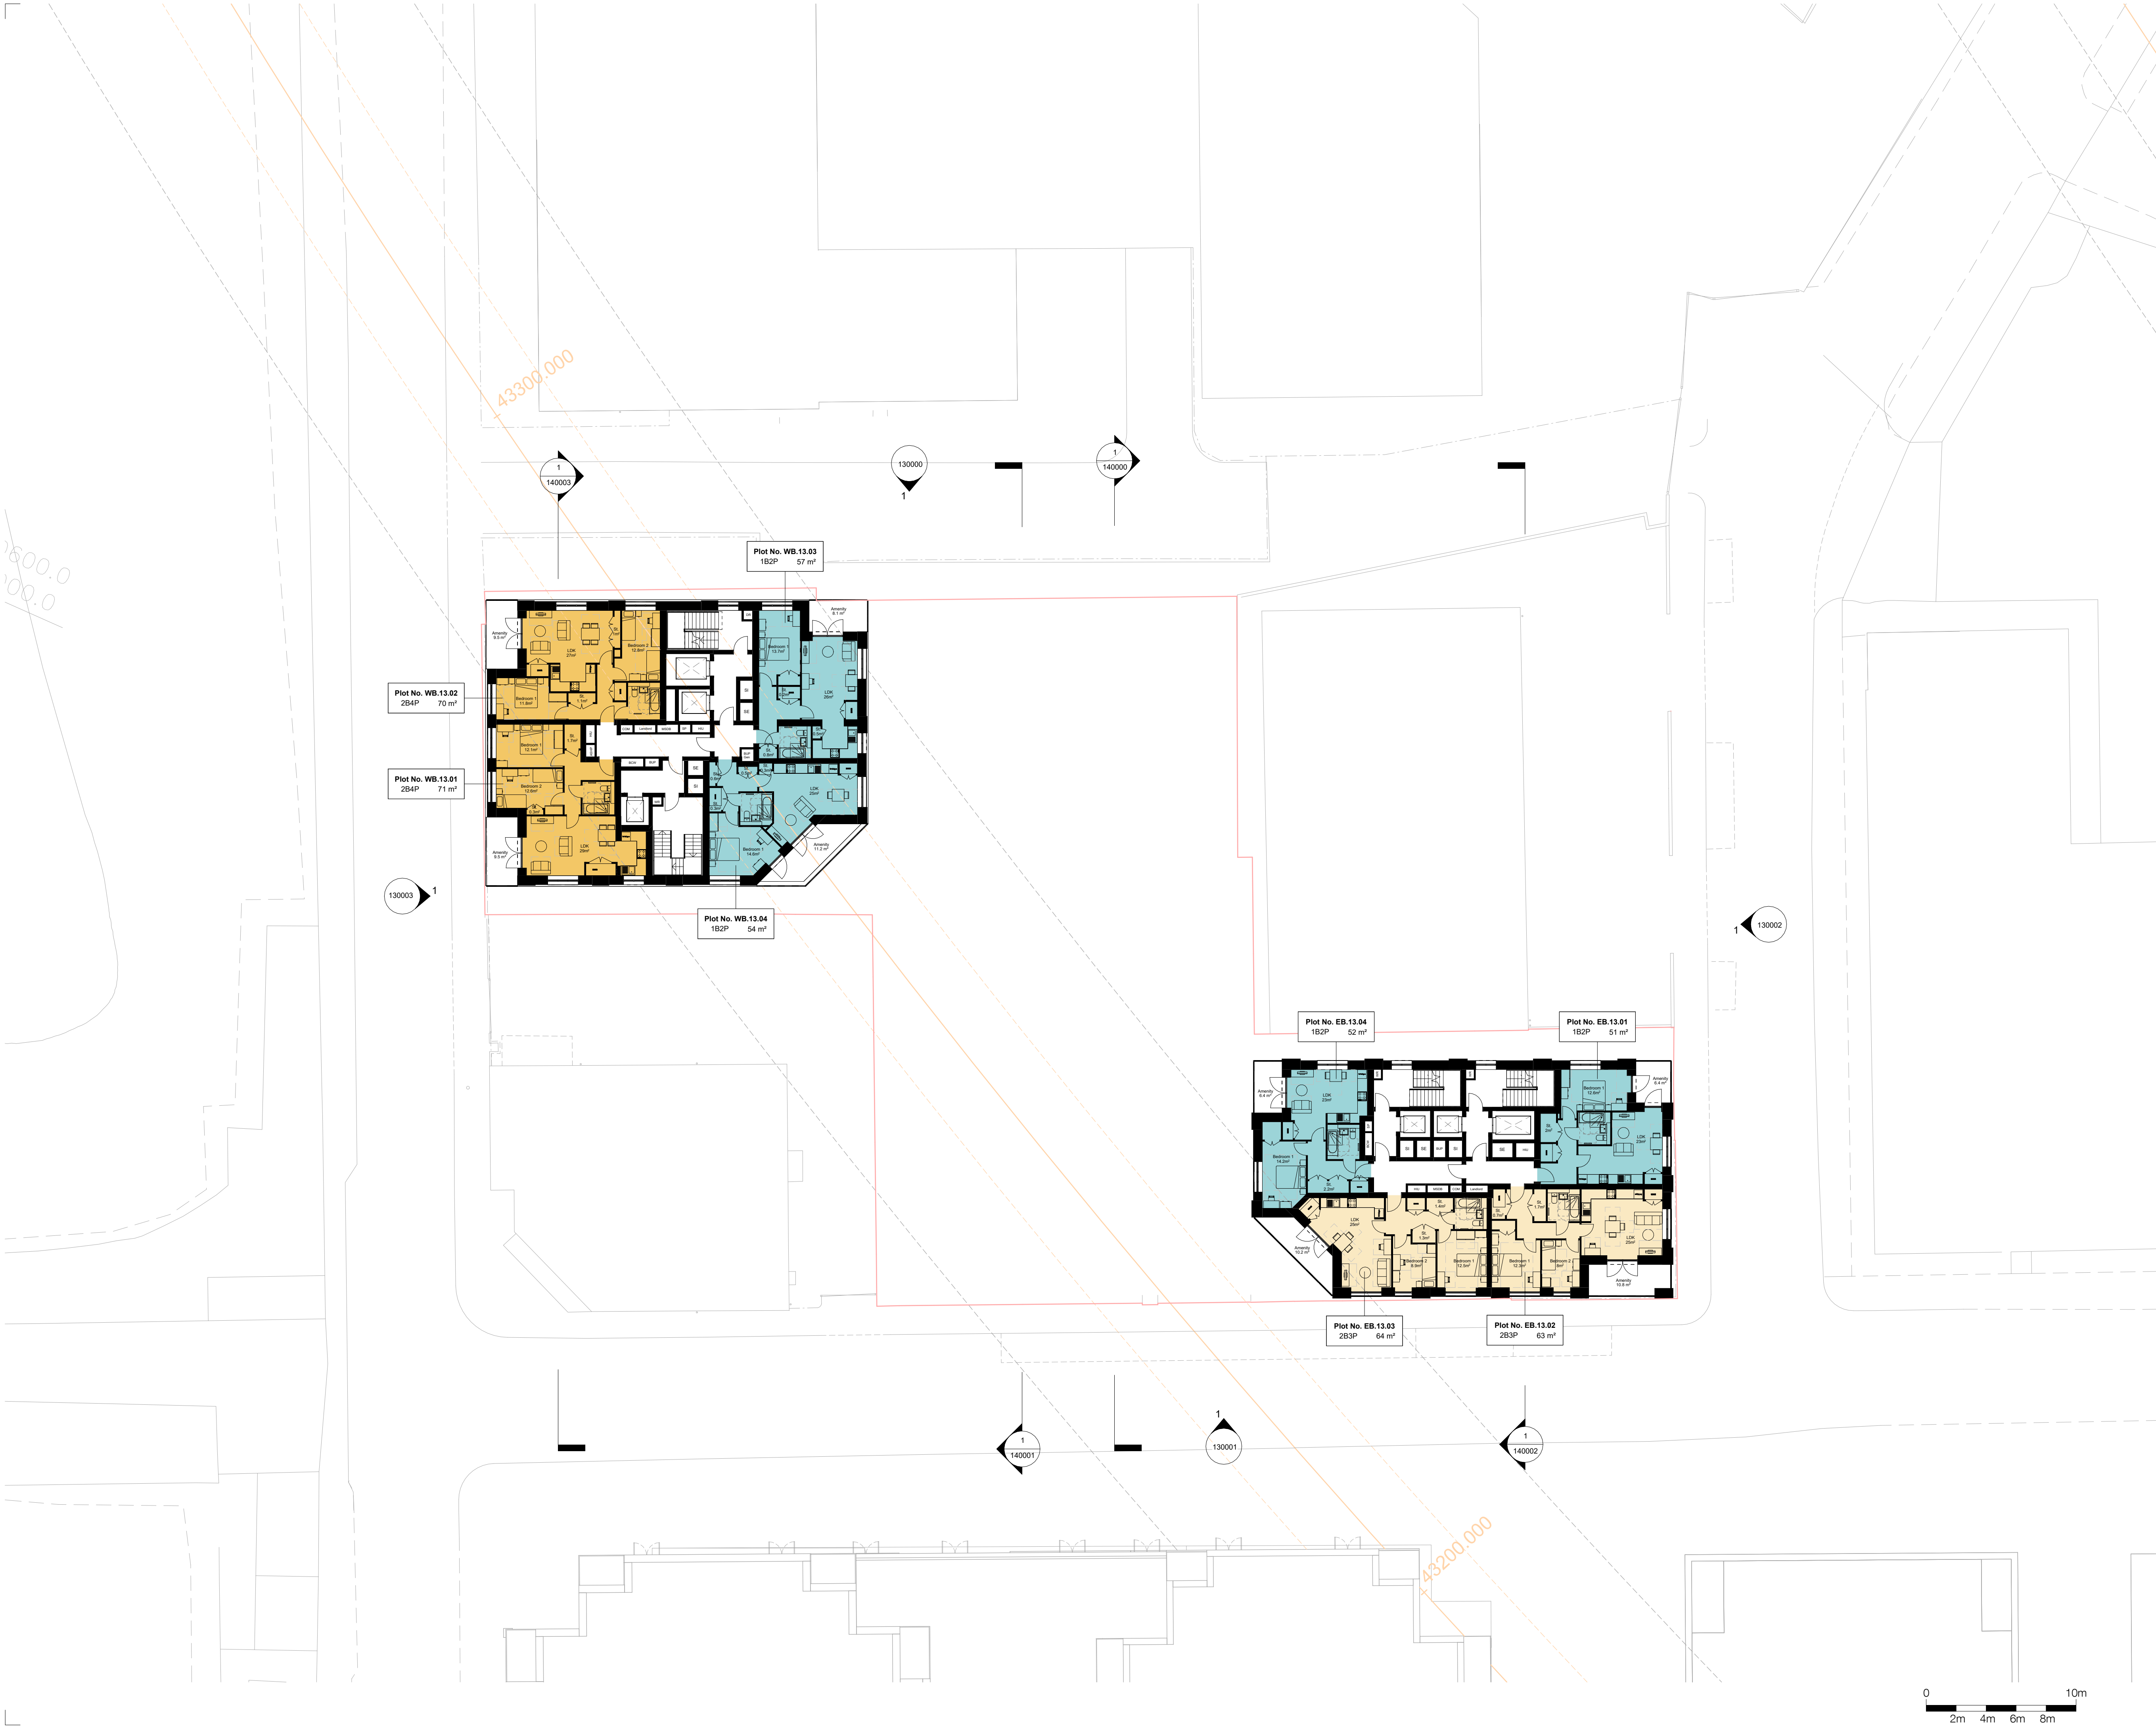

Notes

1. Do not scale this drawing.
2. All dimensions must be checked on site and any discrepancies verified with the architect.
3. Unless shown otherwise, all dimensions are to structural surfaces.
4. Drawing to be read with all other issued information. Any discrepancies to be brought to the attention of the architect.
5. This drawing is the copyright of Levitt Bernstein and may not be copied, altered or reproduced in any form, or passed to a third party without license or written consent.
6. This document is prepared for the sole use of Haringey Council and no liability to any other persons is accepted by Levitt Bernstein. Levitt Bernstein accepts no liability for use of this drawing by parties other than the party for whom it was prepared or for purposes other than those for which it was prepared.

This is not a construction drawing, it is unsuitable for the purpose of construction and must on no account be used as such.

Note: All proposed drawings show emerging context. This includes Clarendon Gasworks Phase 5 proposed massing (as understood to be submitted as part of an RMA) and the buildings approved but yet to be completed: Chocolate Factory Phase 1 building E (HGY/2021/0624), Clarendon Gasworks Phase 4 (HGY/2023/2357).

Riser Types

BCW	Water & Water Meters
LANDLORD	Landlord Distribution Boards
MSDB	Multi Service Distribution Boards
COM	Telecoms, Access control & IRS
SP	Sprinklers
BUP	Backup LV
BUP GEN	Backup Generator Flue
ASHP	Air Source Heat Pumps
HIU	Heat Interface Units
WR	Wet Riser
DR	Dry Riser
SI	Smoke Shaft Intake
SE	Smoke Shaft Extract
AOV	Automatic Opening Vent (Stair Only)

Room Name

1B2P
2B3P
2B4P

Crossrail Tunnel Key

Crossrail tunnel indicated on GA plans to consulting Structural Engineers information and details

— — —	Crossrail Tunnel
— — —	Tunnel Centreline
- - - - -	Exclusion Zone

P03	06.11.25	Planning Issue 02	MF
P02	31.10.25	Planning Issue 01	MF
P01	08.10.25	Draft Stage 3	MF
Rev	Date	Description	Drawn / Checked

Project name

Mallard Place Stage 3

Drawing number Rev

4003A - LB - ZZ - 13 - D - A - 120113 **P03**

Drawing

GA Level 13 - Home Layouts Stage 3


Purpose of issue

Scale Date
1 : 200 @ A1 08.10.25

Client
Haringey Council

London
Thane Studios
2-4 Thane Villas
London N7 7PA
+44 (0)20 7275 7676
Manchester
Bonded Warehouse
18 Lower Byrom Street
Manchester M3 4AP
+44 (0)161 669 6740

Levitt Bernstein
levittbernstein.co.uk

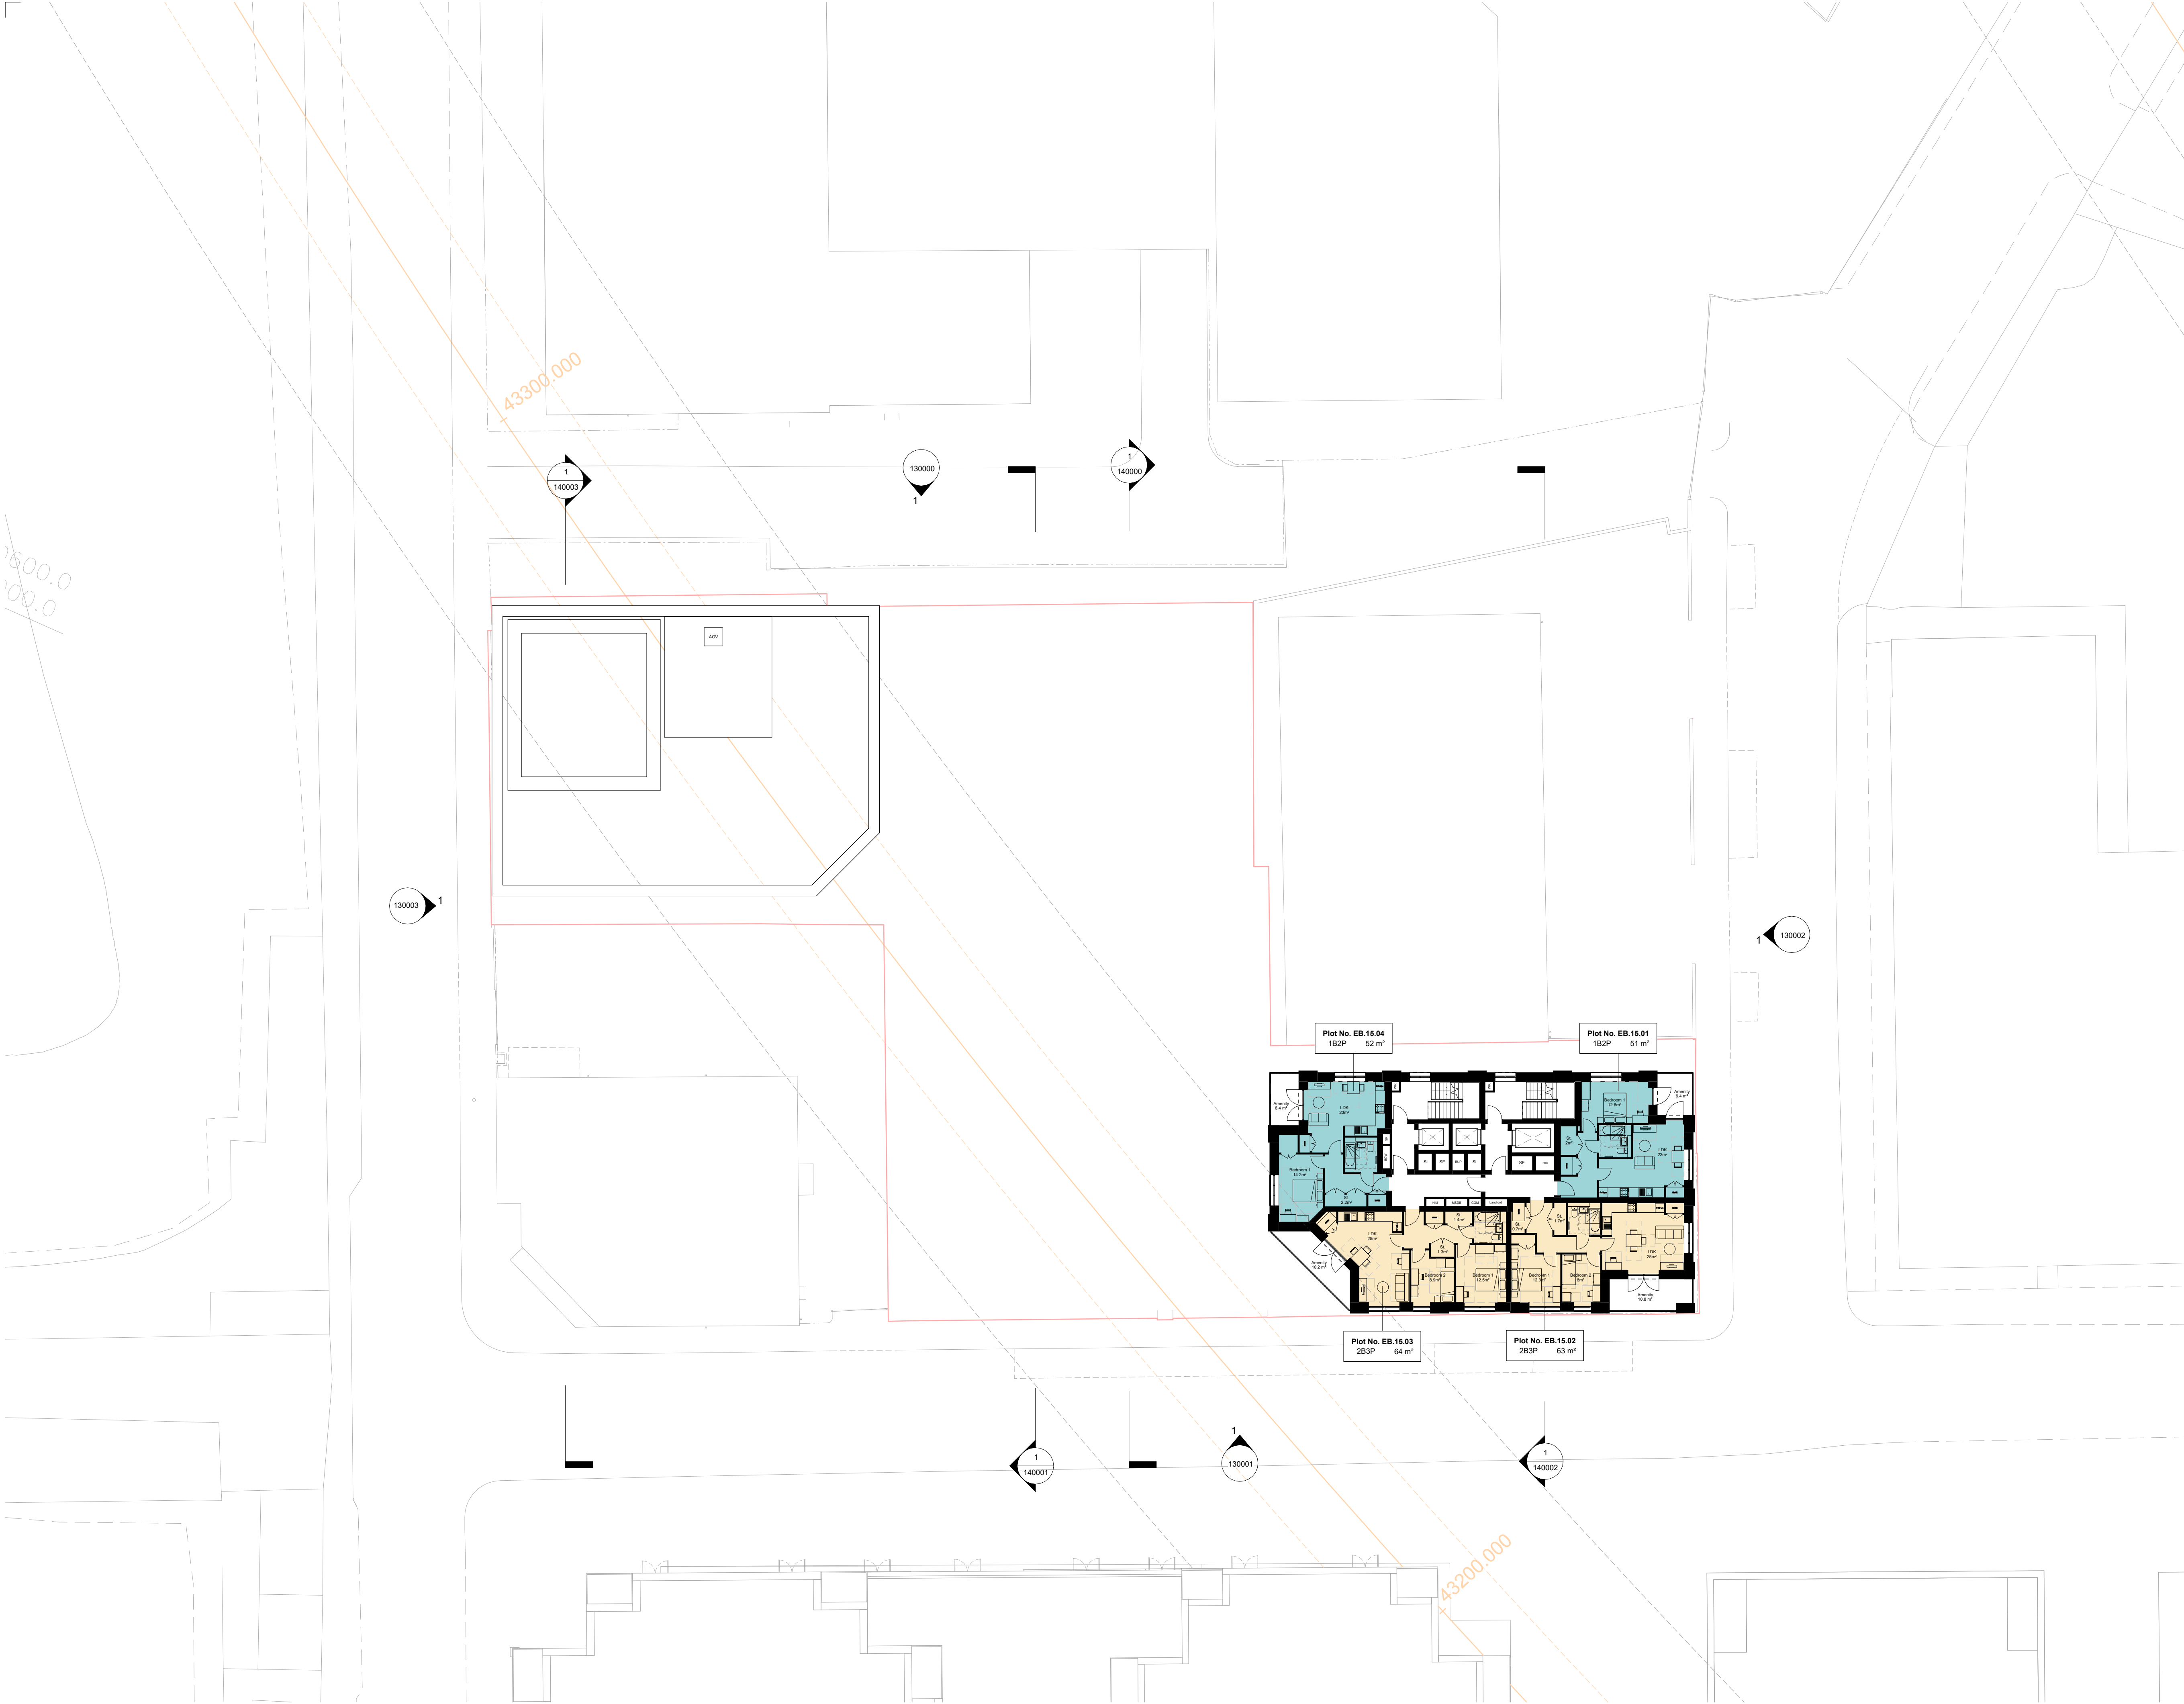

These areas have been prepared for our client and are approximate only. They have been measured from the drawings available at the time and have been generated by the Revit Model. We are not responsible for anomalies caused by areas generated by the Revit Model. Areas are measured and calculated generally in accordance with RICS Code of Measuring Practice, 6th edition, 2007 and have been calculated in metric units. Where imperial units are given, they have been generated and converted from metric by the Revit Model. Areas are measured and calculated generally in accordance with IPMS 3B (RICS Property Measurement, 2nd edition, 2018) can be provided upon request for an additional fee. Areas are rounded to the nearest declared decimal. Construction tolerances, workmanship and design by others may affect the stated areas. All these factors should be considered before making any decisions on the basis of these predictions, whether as to project viability, pre-letting, lease agreements or otherwise, and should include due allowance for the increases and decreases inherent in the design development and construction processes.

Notes

1. Do not scale this drawing.
2. All dimensions must be checked on site and any discrepancies verified with the architect.
3. Unless shown otherwise, all dimensions are to structural surfaces.
4. Drawing to be read with all other issued information. Any discrepancies to be brought to the attention of the architect.
5. This drawing is the copyright of Levitt Bernstein and may not be copied, altered or reproduced in any form, or passed to a third party without license or written consent.
6. This document is prepared for the sole use of Haringey Council and no liability to any other persons is accepted by Levitt Bernstein. Levitt Bernstein accepts no liability for use of this drawing by parties other than the party for whom it was prepared or for purposes other than those for which it was prepared.

This is not a construction drawing, it is unsuitable for the purpose of construction and must on no account be used as such.

Note: All proposed drawings show emerging context. This includes Clarendon Gasworks Phase 5 proposed massing (as understood to be submitted as part of an RMA) and the buildings approved but yet to be completed: Chocolate Factory Phase 1 building E (HGY/2021/0624), Clarendon Gasworks Phase 4 (HGY/2023/2357).

Riser Types

BCW	Water & Water Meters
LANDLORD	Landlord Distribution Boards
MSDB	Multi Service Distribution Boards
COM	Telecoms, Access control & IRS
SP	Sprinklers
BUP	Backup LV
BUP GEN	Backup Generator Flue
ASHP	Air Source Heat Pumps
HIU	Heat Interface Units
WR	Wet Riser
DR	Dry Riser
SI	Smoke Shaft Intake
SE	Smoke Shaft Extract
AOV	Automatic Opening Vent (Stair Only)

Room Name

1B2P	1B2P
2B3P	2B3P

Crossrail Tunnel Key

Crossrail tunnel indicated on GA plans to consulting Structural Engineers information and details

—	Crossrail Tunnel
—	Tunnel Centreline
—	Exclusion Zone

P03	06.11.25	Planning Issue 02	MF
P02	31.10.25	Planning Issue 01	MF
P01	08.10.25	Draft Stage 3	MF
Rev	Date	Description	Drawn / Checked

Project name

Mallard Place Stage 3

Drawing number Rev

4003A - LB - ZZ - 15 - D - A - 120115 **P03**


Drawing

GA Level 15 - Home Layouts Stage 3

Purpose of issue	Date
Scale	1 : 200 @ A1
Client	Haringey Council

London Thane Studios 2-4 Thane Villas London N7 7PA +44 (0)20 7275 7676	Manchester Bonded Warehouse 18 Lower Byrom Street Manchester M3 4AP +44 (0)161 669 6740
--	--

Levitt Bernstein
levittbernstein.co.uk

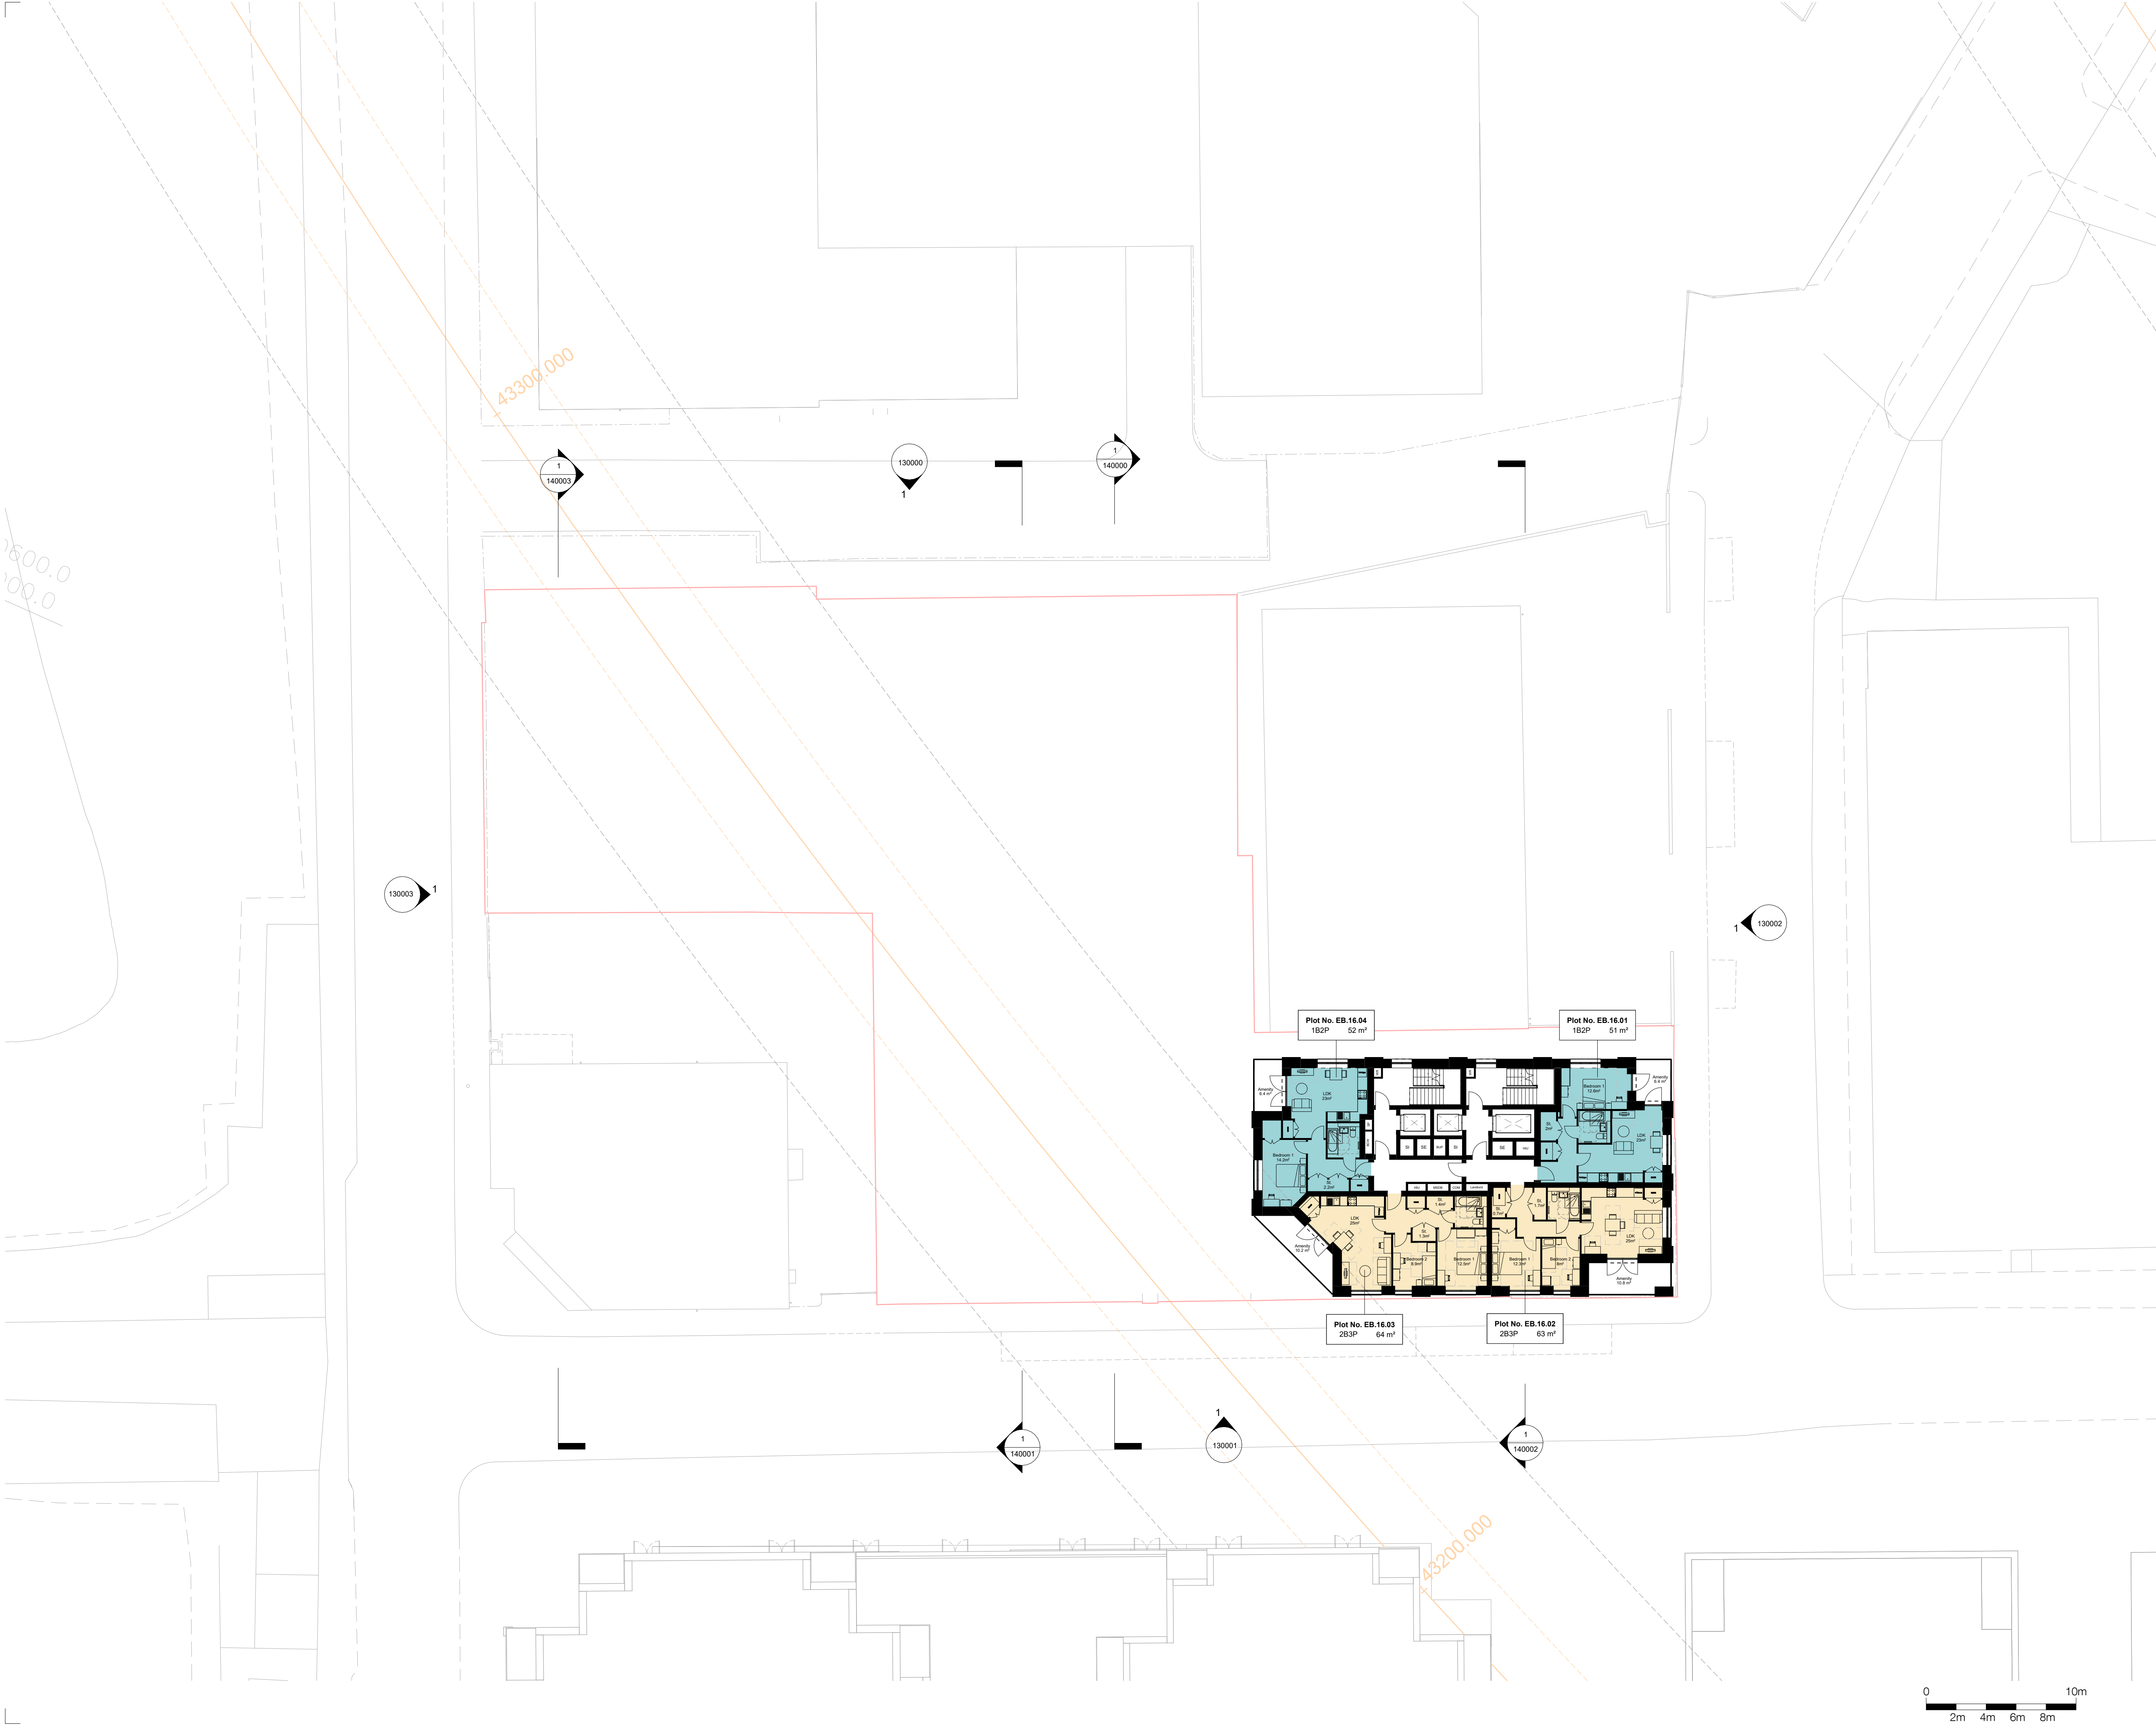

Notes

1. Do not scale this drawing.
2. All dimensions must be checked on site and any discrepancies verified with the architect.
3. Unless shown otherwise, all dimensions are to structural surfaces.
4. Drawing to be read with all other issued information. Any discrepancies to be brought to the attention of the architect.
5. This drawing is the copyright of Levitt Bernstein and may not be copied, altered or reproduced in any form, or passed to a third party without license or written consent.
6. This document is prepared for the sole use of Haringey Council and no liability to any other persons is accepted by Levitt Bernstein. Levitt Bernstein accepts no liability for use of this drawing by parties other than the party for whom it was prepared or for purposes other than those for which it was prepared.

This is not a construction drawing, it is unsuitable for the purpose of construction and must on no account be used as such.

Note: All proposed drawings show emerging context. This includes Clarendon Gasworks Phase 5 proposed massing (as understood to be submitted as part of an RMA) and the buildings approved but yet to be completed: Chocolate Factory Phase 1 building E (HGY/2021/0624), Clarendon Gasworks Phase 4 (HGY/2023/2357).

Riser Types

BCW	Water & Water Meters
LANDLORD	Landlord Distribution Boards
MSDB	Multi Service Distribution Boards
COM	Telecoms, Access control & IRS
SP	Sprinklers
BUP	Backup LV
BUP GEN	Backup Generator Flue
ASHP	Air Source Heat Pumps
HIU	Heat Interface Units
WR	Wet Riser
DR	Dry Riser
SI	Smoke Shaft Intake
SE	Smoke Shaft Extract
AOV	Automatic Opening Vent (Stair Only)

Room Name

1B2P	1B2P
2B3P	2B3P

Crossrail Tunnel Key

Crossrail tunnel indicated on GA plans to consulting Structural Engineers information and details

- - -	Crossrail Tunnel
- - -	Tunnel Centreline
- - -	Exclusion Zone

P03	06.11.25	Planning Issue 02	MF
P02	31.10.25	Planning Issue 01	MF
P01	08.10.25	Draft Stage 3	MF
Rev	Date	Description	Drawn / Checked

Project name

Mallard Place
Stage 3

Drawing number Rev

4003A - LB - ZZ - 16 - D - A - 120116 P03

Drawing

GA Level 16 - Home Layouts

Purpose of issue

Stage 3

Scale Date
1 : 200 @ A1 08.10.25

Client
Haringey Council

London
Thane Studios
2-4 Thane Villas
London N7 7PA
+44 (0)20 7275 7676
Manchester
Bonded Warehouse
18 Lower Byrom Street
Manchester M3 4AP
+44 (0)161 669 6740
Levitt Bernstein
levittbernstein.co.uk

1. Do not scale this drawing.
2. All dimensions must be checked on site and any discrepancies verified with the architect.
3. Unless shown otherwise, all dimensions are to structural surfaces.
4. Drawing to be read with all other issued information. Any discrepancies to be brought to the attention of the architect.
5. This drawing is the copyright of Levitt Bernstein and may not be copied, altered or reproduced in any form, or passed to a third party without license or written consent.
6. This document is prepared for the sole use of
Haringey Council
and may not be used by any other persons is accepted by Levitt Bernstein. Levitt Bernstein accepts no liability for use of this drawing by parties other than the party for whom it was prepared or for purposes other than those for which it was prepared.

Note: All proposed drawings show emerging context. This includes Clarendon Gasworks Phase 5 proposed massing (as understood to be submitted as part of an RMA) and the buildings approved but yet to be completed: Chocolate Factory Phase 1 building E (HGY/2021/0624), Clarendon Gasworks Phase 4 (HGY/2023/2357).

BCW
LANDLORD
MSDB
COM
SP
BUP
BUP GEN

BCW	Water & Water Meters
LANDLORD	Landlord Distribution Boards
MSDB	Multi Service Distribution Boards
COM	Telecoms, Access control & IRS
SP	Sprinklers
BUP	Backup LV
BUP GEN	Backup Generator Flue

ASHP Air Source Heat Pumps
HIU Heat Interface Units

WR Wet Riser
DR Dry Riser

SI	Smoke Shaft Intake
SE	Smoke Shaft Extract
AOV	Automatic Opening Vent (Stair Only)

 1B2F

Crossrail tunnel indicated on GA plans to consulting Structural Engineers information and details

- — — Crossrail Tunnel
- Tunnel Centreline
- — — Exclusion Zone

P03	06.11.25	Planning Issue 02	MF
P02	31.10.25	Planning Issue 01	MF
P01	08.10.25	Draft Stage 3	MF
Rev	Date	Description	Drawn / Checked

Project name

Stage 3

Drawing number Rev

Drawing

GA Level 17 - Home Layouts

Purpose of

Scale Date
1 : 200 @ A1 08.10.25

Client
Haringey Council

London
Thane Studios
2-4 Thane Villas
London N7 7PA
+44 (0)20 7275 7676

Manchester
Bonded Warehouse
18 Lower Byrom Street
Manchester M3 4AP
+44 (0)161 669 8740

Levitt Bernstein
levittbernstein.co.uk

These areas have been prepared for our client and are approximate only. They have been measured from the drawings available at the time and have been generated by the Revit Model. We are not responsible for anomalies caused by areas generated by the Revit Model. Measurements are measured and calculated generally in accordance with RICS Code of Measuring Practice, 8th edition, 2007 and 2018. Where Imperial units are given, they have been generated and converted from metric by the Revit Model. Measurements measured in accordance with IPMS 3B (RICS Property Measurement, 2nd edition, 2018) can be provided upon request for additional fee. Areas are rounded to the nearest declared decimal/Construction Tolerances, workmanship and design by others may affect the stated areas. For existing buildings, the building may present anomalies in relation to surveyed/drawn plans that may also affect the stated areas. All these factors should be considered before making any decisions on the basis of these predictions, whether as to project viability, pre-letting, lease agreements or otherwise, and should include due allowance for the increases and decreases inherent in the design development and construction processes.

1. Do not scale this drawing.
2. All dimensions must be checked on site and any discrepancies verified with the architect.
3. Unless shown otherwise, all dimensions are to structural surfaces.
4. Drawing to be read with all other issued information. Any discrepancies to be brought to the attention of the architect.
5. This drawing is the copyright of Levitt Bernstein and may not be copied, altered or reproduced in any form, or passed to a third party without license or written consent.
6. This document is prepared for the sole use of the Houghton Council and is not to be used by any other persons is accepted by Levitt Bernstein. Levitt Bernstein accepts no liability for use of this drawing by parties other than the party for whom it was prepared or for purposes other than those for which it was prepared.

Riser Types

BCW	Water & Water Meters
LANDLORD	Landlord Distribution Boards
MSDB	Multi Service Distribution Boards
COM	Telecoms, Access control & IRS
SP	Sprinklers
BUF	Backup LV
BUF GEN	Backup Generator Flue
ASHP	Air Source Heat Pumps
HIU	Heat Interface Units
WR	Wet Riser
DR	Dry Riser
SI	Smoke Shaft Intake
SE	Smoke Shaft Extract
AOV	Automatic Opening Vent (Stair Only)

1B2P
2B3P

Crossrail tunnel indicated on GA plans to consulting Structural Engineers information and details

- Crossrail Tunnel
 Tunnel Centreline
 Exclusion Zone

Project name

Drawing number _____ Rev _____

Drawing

Purpose of Stage 3


Client
Haringey Council

London
Thane Studios
2-4 Thane Villas
London N7 7PA
+44 (0)20 7275 7676

Manchester
Bonded Warehouse
18 Lower Byrom Street
Manchester M3 4AP
+44 (0)161 669 8740

Levitt Bernstein
levittbernstein.co.uk

Additional fees are prepared for our client and are approximate only. They have been measured from the drawings available at the time and have been generated by the Revit Model. We are not responsible for anomalies caused by areas generated by the Revit Model. Measurements are measured and calculated generally in accordance with RICS Code of Measuring Practice, 6th edition, 2007 and 2018. Where imperial units are given, they have been generated and converted from metric by the Revit Model. Measurements are measured in accordance with IPMS 3B (RICS Property Measurement, 2nd edition, 2018) can be provided upon request for the above areas. Areas are rounded to the nearest declared decimal/Construction tolerances, workmanship and design by which they affect the stated areas. For existing buildings, the building may present anomalies in relation to surveyed/drawn plans that may also affect the stated areas. All these factors should be considered before making any decisions on the basis of these predictions, whether as to project viability, pre-letting, lease agreements or otherwise, and should include due allowance for the increases and decreases inherent in the design development and construction processes.

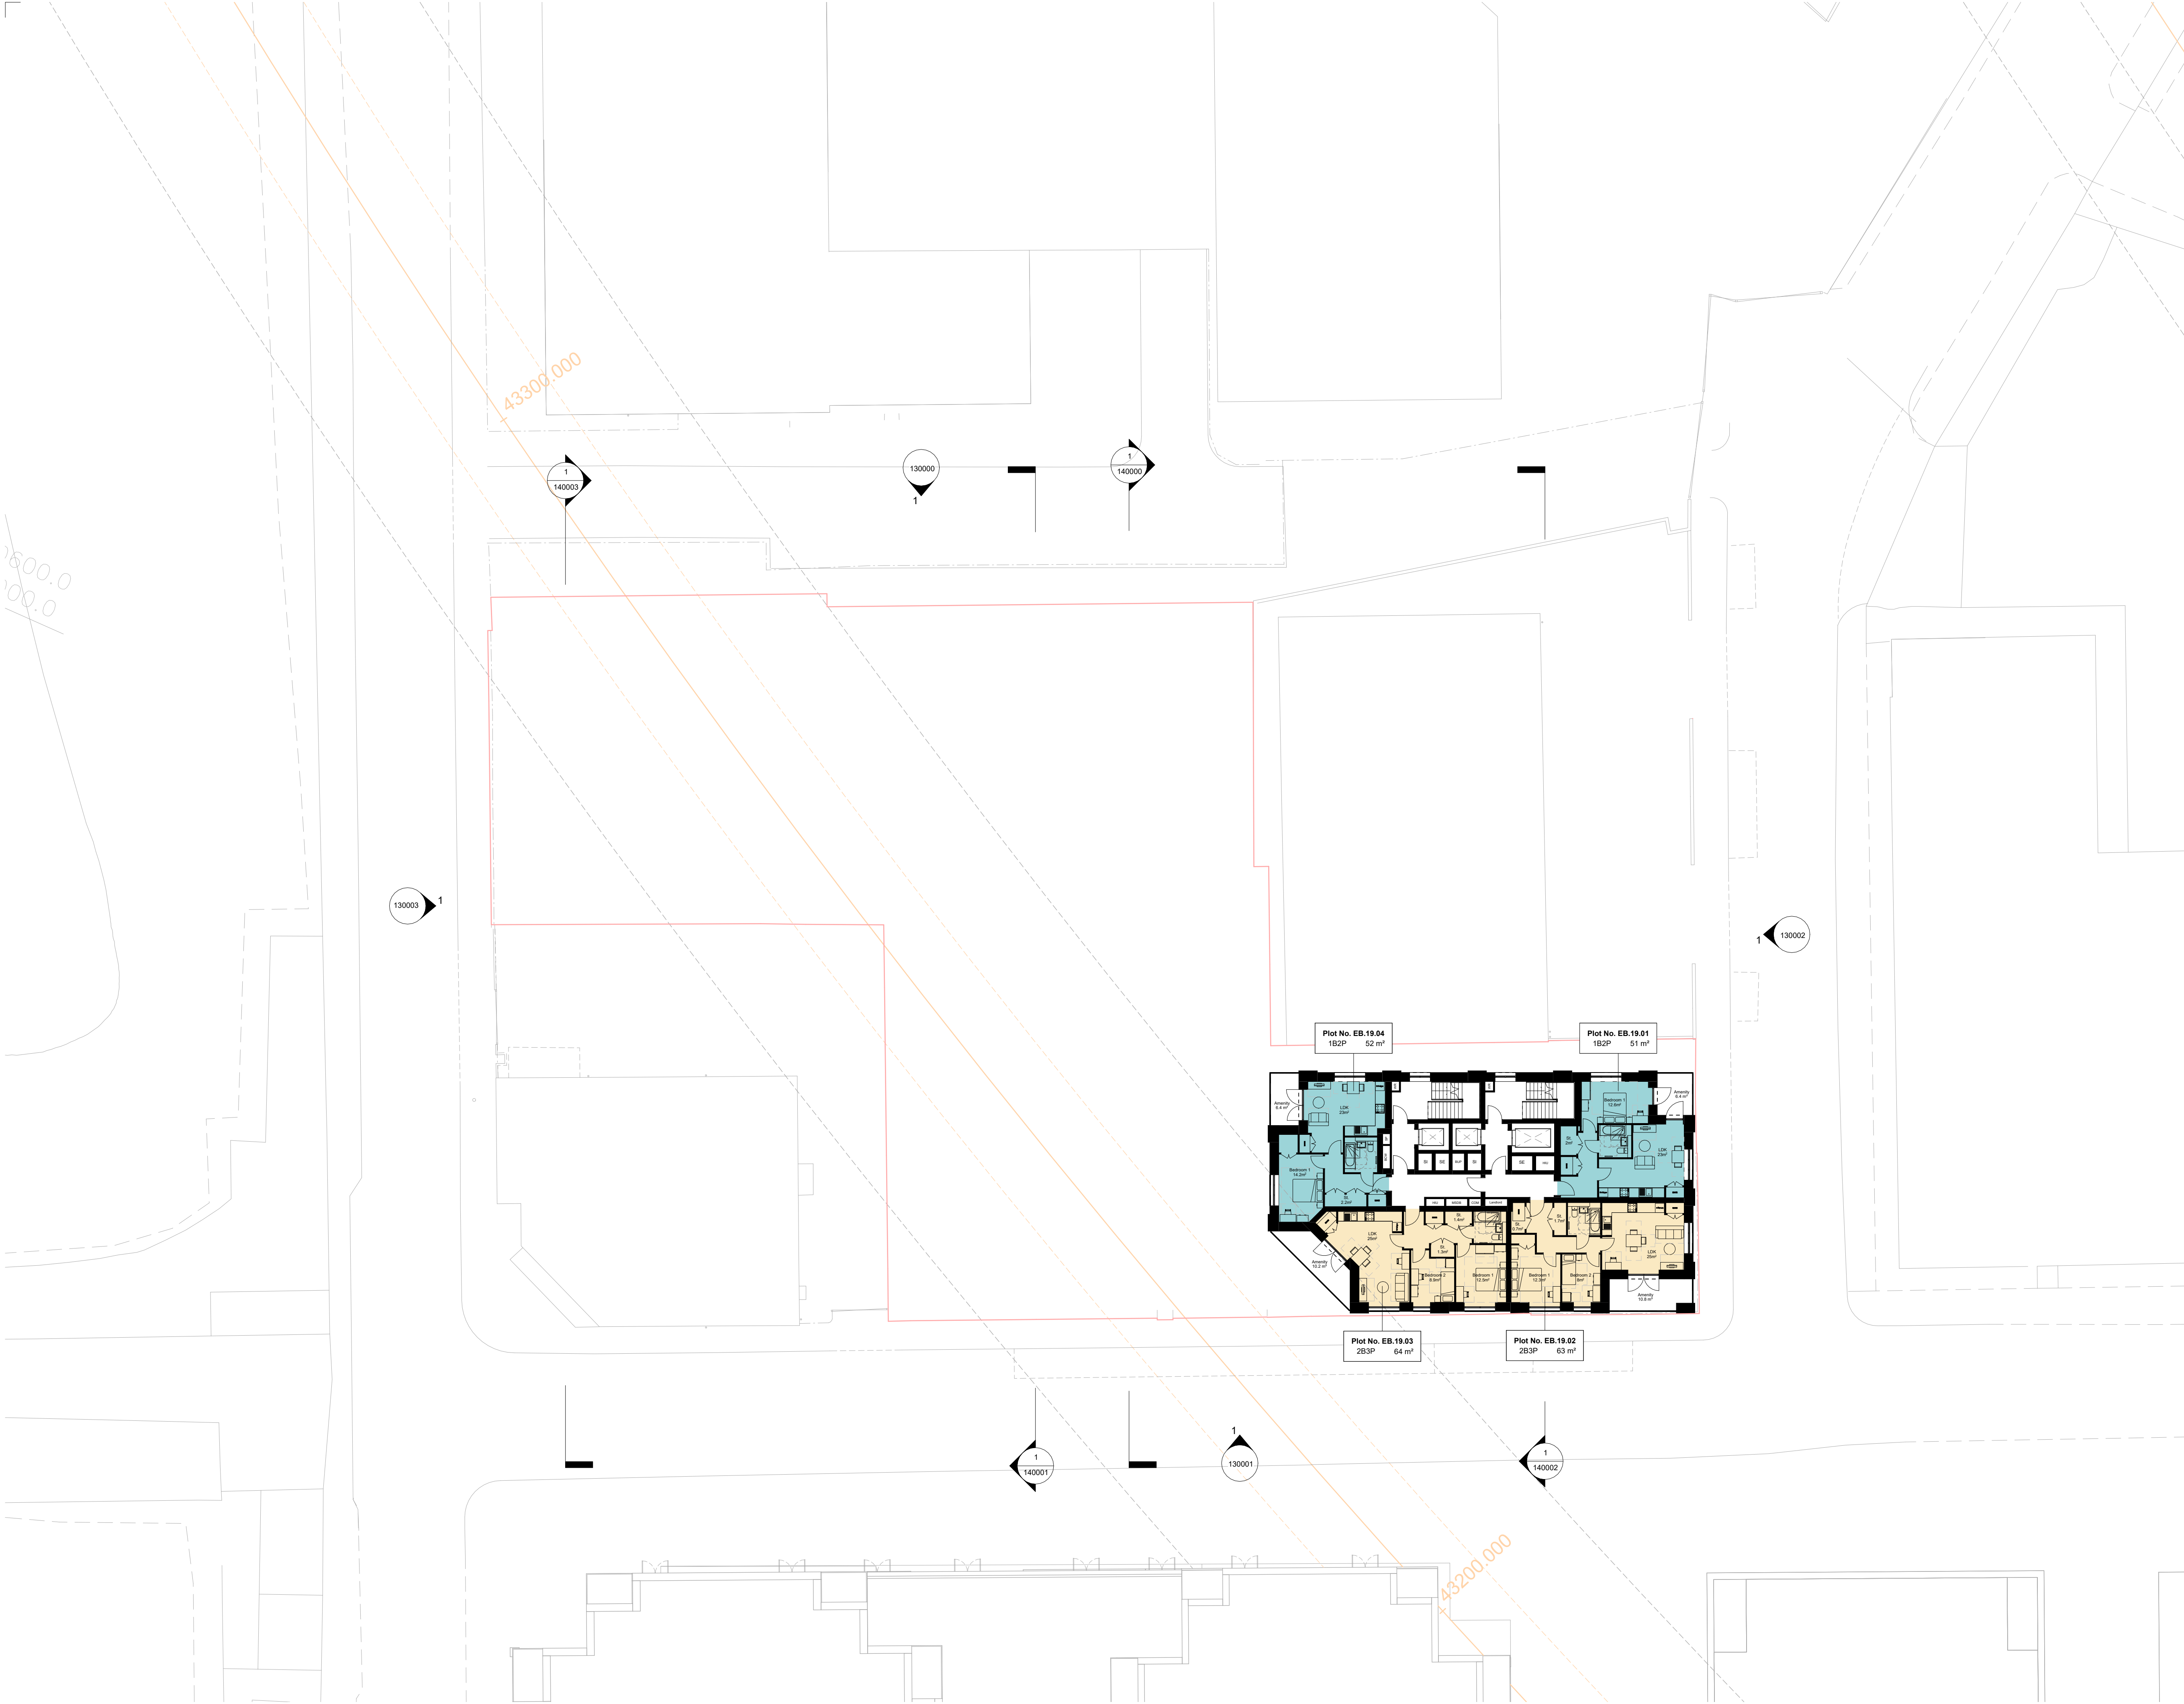

Notes

1. Do not scale this drawing.
2. All dimensions must be checked on site and any discrepancies verified with the architect.
3. Unless shown otherwise, all dimensions are to structural surfaces.
4. Drawing to be read with all other issued information. Any discrepancies to be brought to the attention of the architect.
5. This drawing is the copyright of Levitt Bernstein and may not be copied, altered or reproduced in any form, or passed to a third party without license or written consent.
6. This document is prepared for the sole use of Haringey Council and no liability to any other persons is accepted by Levitt Bernstein. Levitt Bernstein accepts no liability for use of this drawing by parties other than the party for whom it was prepared or for purposes other than those for which it was prepared.

This is not a construction drawing, it is unsuitable for the purpose of construction and must on no account be used as such.

Note: All proposed drawings show emerging context. This includes Clarendon Gasworks Phase 5 proposed massing (as understood to be submitted as part of an RMA) and the buildings approved but yet to be completed: Chocolate Factory Phase 1 building E (HGY/2021/0624), Clarendon Gasworks Phase 4 (HGY/2023/2357).

Riser Types

BCW	Water & Water Meters
LANDLORD	Landlord Distribution Boards
MSDB	Multi Service Distribution Boards
COM	Telecoms, Access control & IRS
SP	Sprinklers
BUP	Backup LV
BUP GEN	Backup Generator Flue
ASHP	Air Source Heat Pumps
HIU	Heat Interface Units
WR	Wet Riser
DR	Dry Riser
SI	Smoke Shaft Intake
SE	Smoke Shaft Extract
AOV	Automatic Opening Vent (Stair Only)

Room Name

1B2P
2B3P

Crossrail Tunnel Key

Crossrail tunnel indicated on GA plans to consulting Structural Engineers information and details

—	Crossrail Tunnel
—	Tunnel Centreline
—	Exclusion Zone

P03	06.11.25	Planning Issue 02	MF
P02	31.10.25	Planning Issue 01	MF
P01	08.10.25	Draft Stage 3	MF
Rev	Date	Description	Drawn / Checked

Project name

Mallard Place Stage 3

Drawing number Rev

4003A - LB - ZZ - 19 - D - A - 120119 P03

Drawing

GA Level 19 - Home Layouts


Purpose of issue
Stage 3

Scale Date
1 : 200 @ A1 08.10.25

Client
Haringey Council

London
Thane Studios
2-4 Thane Villas
London N7 7PA
+44 (0)20 7275 7676
Manchester
Bonded Warehouse
18 Lower Byrom Street
Manchester M3 4AP
+44 (0)161 669 6740

Levitt Bernstein
levittbernstein.co.uk

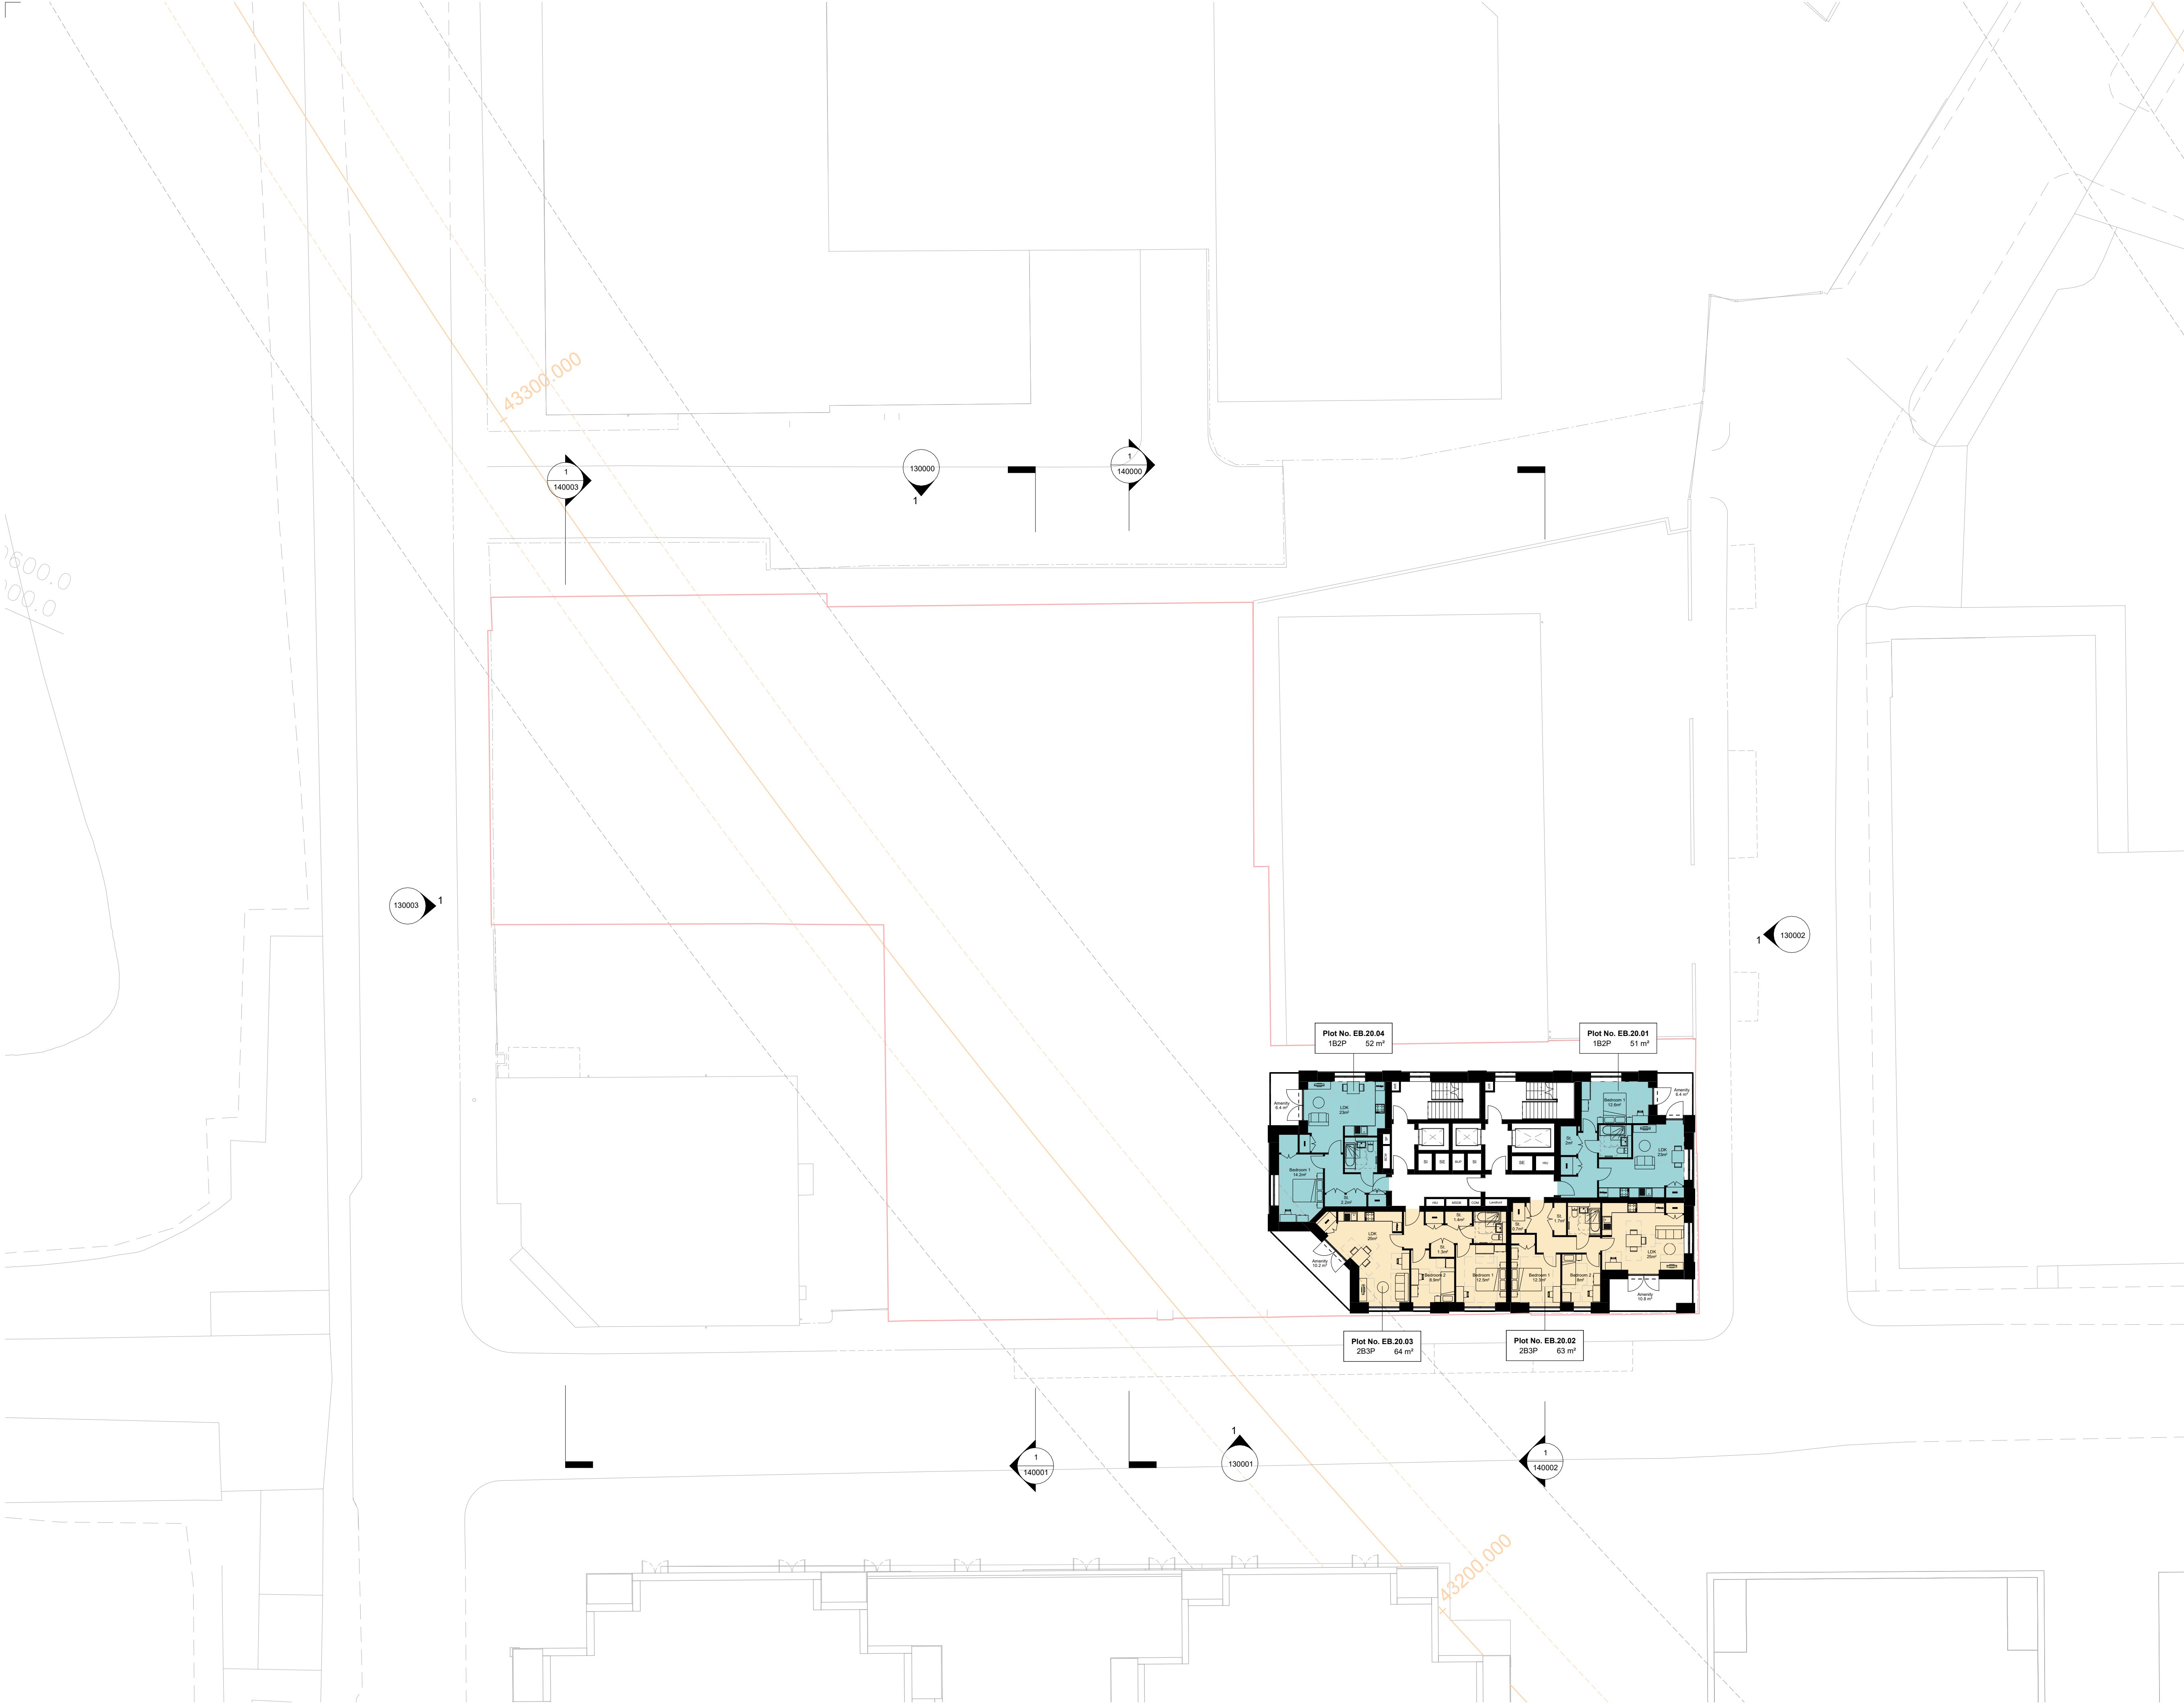

Notes

1. Do not scale this drawing.
2. All dimensions must be checked on site and any discrepancies verified with the architect.
3. Unless shown otherwise, all dimensions are to structural surfaces.
4. Drawing to be read with all other issued information. Any discrepancies to be brought to the attention of the architect.
5. This drawing is the copyright of Levitt Bernstein and may not be copied, altered or reproduced in any form, or passed to a third party without license or written consent.
6. This document is prepared for the sole use of Haringey Council and no liability to any other persons is accepted by Levitt Bernstein. Levitt Bernstein accepts no liability for use of this drawing by parties other than the party for whom it was prepared or for purposes other than those for which it was prepared.

This is not a construction drawing, it is unsuitable for the purpose of construction and must on no account be used as such.

Note: All proposed drawings show emerging context. This includes Clarendon Gasworks Phase 5 proposed massing (as understood to be submitted as part of an RMA) and the buildings approved but yet to be completed: Chocolate Factory Phase 1 building E (HGY/2021/0624), Clarendon Gasworks Phase 4 (HGY/2023/2357).

Riser Types

BCW	Water & Water Meters
LANDLORD	Landlord Distribution Boards
MSDB	Multi Service Distribution Boards
COM	Telecoms, Access control & IRS
SP	Sprinklers
BUP	Backup LV
BUP GEN	Backup Generator Flue
ASHP	Air Source Heat Pumps
HIU	Heat Interface Units
WR	Wet Riser
DR	Dry Riser
SI	Smoke Shaft Intake
SE	Smoke Shaft Extract
AOV	Automatic Opening Vent (Stair Only)

Room Name

1B2P
2B3P

Crossrail Tunnel Key

Crossrail tunnel indicated on GA plans to consulting Structural Engineers information and details

— — —	Crossrail Tunnel
— — —	Tunnel Centreline
— — —	Exclusion Zone

P03	06.11.25	Planning Issue 02	MF
P02	31.10.25	Planning Issue 01	MF
P01	08.10.25	Draft Stage 3	MF
Rev	Date	Description	Drawn / Checked

Project name

Mallard Place
Stage 3

Drawing number Rev

4003A - LB - ZZ - 20 - D - A - 120120 P03

Drawing

GA Level 20 - Home Layouts

Purpose of issue

Stage 3

Scale Date
1 : 200 @ A1 08.10.25

Client
Haringey Council

London
Thane Studios
2-4 Thane Villas
London N7 7PA
+44 (0)20 7275 7676
Manchester
Bonded Warehouse
18 Lower Byrom Street
Manchester M3 4AP
+44 (0)161 669 6740
Levitt Bernstein
levittbernstein.co.uk

1. Do not scale this drawing.
2. All dimensions must be checked on site and any discrepancies verified with the architect.
3. Unless shown otherwise, all dimensions are to structural surfaces.
4. Drawing to be read with all other issued information. Any discrepancies to be brought to the attention of the architect.
5. This drawing is the copyright of Levitt Bernstein and may not be copied, altered or reproduced in any form, or passed to a third party without license or written consent.
6. This document is prepared for the sole use of the Hagerman Council and is not to be used by Levitt Bernstein. Levitt Bernstein accepts no liability for use of this drawing by parties other than the party for whom it was prepared or for purposes other than those for which it was prepared.

Note: All proposed drawings show emerging context. This includes Clarendon Gasworks Phase 5 proposed massing (as understood to be submitted as part of an RMA) and the buildings approved but yet to be completed: Chocolate Factory Phase 1 building E (HGY/2021/0624), Clarendon Gasworks Phase 4 (HGY/2023/2357).

BCW	Water & Water Meters
LANDLORD	Landlord Distribution Boards
MSDB	Multi Service Distribution Boards
COM	Telecoms, Access control & IRS
SP	Sprinklers
BUP	Backup LV
BUP GEN	Backup Generator Flue

WR Wet Rise
DR Dry Riser

Room Name

2B3F

Crossrail tunnel indicated on GA plans to consulting Structural Engineers information and details

 Tunnel Centreline

— — — Exclusion Zone

P03	06.11.25	Planning Issue 02	MF
P02	31.10.25	Planning Issue 01	MF
P01	08.10.25	Draft Stage 3	MF
Rev	Date	Description	Drawn / Checked

Project name

Stage 3

Drawing number Rev

Drawing

Purpose of

Scale Date
1 : 200 @ A1 08.10.25

Client
Haringey Council

London
Thane Studios
2-4 Thane Villas
London N7 7PA
+44 (0)20 7275 7676

Manchester
Bonded Warehouse
18 Lower Byrom Street
Manchester M3 4AP
+44 (0)161 669 8740

Levitt Bernstein
levittbernstein.co.uk

Additional fees are prepared for our client and are approximate only. They have been measured from the drawings available at the time and have been generated according to the Revit Model. We are not responsible for anomalies caused by areas generated by the Revit software measured and calculated generally in accordance with RICS Code of Measuring Practice, 6th edition, 2007 and 2018, where imperial units are given, they have been generated and converted from metric by the Revit Model. Measurements measured in accordance with IPMS 3b (RICS Property Measurement, 2nd edition, 2018) can be provided upon request for areas above the floor level. Additional fees are prepared for the nearest declared decimal/Construction tolerances, workmanship and design by others may affect the stated areas. For existing buildings, the building may present anomalies in relation to surveyed/drawn plans that may also affect the stated areas. All these factors should be considered before making any decisions on the basis of these predictions, whether as to project viability, pre-letting, lease agreements or otherwise, and should include due allowance for the increases and decreases inherent in the design development and construction process.

C:\Revit Local\4003A_Mallard Place-Building-R24-Central_hannah.williams8B99N.rvt

1 Mallard Place, Chocolate Factory – Phase 2

Local Planning Authority: Haringey

Local Planning Authority reference: HGY/2025/3217

Strategic planning application stage 2 referral

Town & Country Planning Act 1990 (as amended); Greater London Authority Acts 1999 and 2007; Town & Country Planning (Mayor of London) Order 2008.

The proposal

Full planning application for the demolition of existing buildings on the site to deliver 150 affordable social-rented dwellings (Use Class C3) within buildings up to a maximum of 22 storeys, with 539sqm flexible workspace (Use Class E) on the ground and first floors.

The applicant

The applicant is **Haringey Council**, and the architect is **Levitt Bernstein**.

Key dates

GLA pre-application meetings: 18 March 2025 and 7 October 2025

GLA stage 1 report: 12 January 2026

LPA Planning Committee decision: 5 February 2026

Strategic issues summary

Land use principles: The redevelopment of the site to provide affordable housing and flexible workspace within a town centre and an Opportunity Area is strongly supported in strategic planning terms. The provision of affordable workspace is secured. A replacement premises for the existing SEN education use is also secured.

Affordable housing: The proposal to deliver 150 affordable housing units (100% by HR) consisting of 100% (low-cost) social-rented homes is strongly supported and secured.

Urban design and heritage: Whilst the site is not identified as suitable for tall buildings the proposal came forward in the context of an emerging tall building cluster, and the heights are acceptable in this context. Less than substantial harm caused to the settings of Alexandra Park (Registered Park and Garden), is outweighed by public benefits including the provision of 100% affordable housing.

Transport: Acceptable further information on ATZ and trip generation, and mitigation measures to local connectivity to align with ongoing initiatives provided. A parking design and management, travel, delivery and servicing, and construction logistics, plans are secured by conditions. Financial contributions are secured for the implementation of the mitigation measures agreed.

Environment: Outstanding issues are acceptably resolved and secured by conditions.

The Council's decision

In this instance Haringey Council has resolved to grant permission subject to planning conditions and conclusion of a Section 106 legal agreement.

Recommendation

That Haringey Council be advised that the Mayor is content for the Council to determine the case itself, subject to any action that the Secretary of State may take and does not therefore wish to direct refusal.

Context

1. On 2 December 2025, the Mayor of London received documents from Haringey Council notifying him of a planning application of potential strategic importance to develop the above site for the above uses. This was referred to the Mayor under the following Categories of the Schedule to the Order 2008:
 - **Category 1A** "Development which comprises or includes the provision of more than 150 houses, flats, or houses and flats."
 - **Category 1B:** "Development (other than development which only comprises the provision of houses, flats, or houses and flats) which comprises or includes the erection of a building or buildings outside Central London and with a total floorspace of more than 15,000 square metres."
 - **Category 1C:** "Development which comprises or includes the erection of a building of one or more of the following descriptions- (c) the building is more than 30 metres high and is outside the City of London."
2. On 12 January 2026, the Deputy Mayor for Planning, Regeneration and Skills, acting under delegated authority, considered planning report GLA/2025/1008/01 (link to report [here](#))¹ and subsequently advised Haringey Council that the application does not fully comply with these policies, as summarised below:
 - **Land use principles:** The redevelopment of the site to provide affordable housing and flexible workspace within a town centre and an Opportunity Area is strongly supported in strategic planning terms. The provision of affordable workspace is welcomed. It must however be demonstrated that the application will secure replacement premises for the existing SEN education use, or else robust evidence submitted that this use is not required in the borough.
 - **Affordable housing:** The proposal is to deliver 150 affordable housing units consisting of 100% social-rented homes. This is strongly supported, and the scheme can follow the Fast Track Route.
 - **Urban design and heritage:** Whilst the site is not identified as suitable for tall buildings the proposal is coming forward in the context of an emerging tall building cluster and the heights are acceptable in this context. A very

¹ <https://planapps.london.gov.uk/planningapps/HGY-2025-3217>

low level of harm could be caused to the settings of Alexandra Park (Registered Park and Garden) which could be outweighed by the public benefits of the proposal.

- **Transport:** Further information is required on ATZ and trip generation, and mitigation to local connectivity to align with ongoing initiatives. Parking design and management, travel, delivery and servicing, and construction logistics, plans should be secured by condition.
 - **Environment and sustainable infrastructure:** Further information is required, and matters raised should be addressed prior to the Mayor's decision-making stage.
3. The essentials of the case with regard to the proposal, the site, case history, strategic planning issues and relevant policies and guidance are as set out therein, unless otherwise stated in this report.
 4. On 5 February 2026, Haringey Council decided that it was minded to grant permission for the application subject to planning conditions and conclusion of a Section 106 agreement, and on 18 March 2026, it advised the Mayor of this decision. Under the provisions of Article 5 of the Town & Country Planning (Mayor of London) Order 2008 the Mayor may allow the draft decision to proceed unchanged; direct Haringey Council under Article 6 to refuse the application; or issue a direction to Haringey Council under Article 7 that he is to act as the Local Planning Authority for the purposes of determining the application and any connected application. The Mayor has until 31 March 2026 to notify the Council of his decision and to issue any direction.
 5. The decision on this case, and the reasons, will be made available on the City Hall website: <https://planapps.london.gov.uk/>

Response to neighbourhood consultation

6. Haringey Council publicised the application by sending notification letters to local addresses and issuing site and press notices. The relevant statutory bodies were also consulted. Copies of all responses to public consultation, and any other representations made on the case, have been made available to the GLA.
7. Following the neighbourhood consultation process Haringey Council has not received any response from residents or social groups in the neighbourhood.

Responses from statutory bodies and other organisations

Thames Water

8. No objection subject to conditions. The proposed conditions are secured.

Metropolitan Police Designing out crime

9. No objections, subject to conditions and informative, which are secured.

Environment Agency

10. No comments.

Crossrail 2 Safeguarding

11. No objections, subject to conditions and informative, which are secured.

Network Rail

12. No objection.

London Underground/ DLR Infrastructure Protection

13. No objection.

Historic England

14. No comment.

Greater London Archaeological Advisory Service

15. No comment.

Natural England

16. No objection.

National Health Service London Healthy Development Unit

17. Requested is the Council secure £83,000 within the S106 agreement to be paid on commencement and indexed linked to building costs. (Council Officer's comment: Consistent with the position on other applications and as set out in the Council's latest published Annual Infrastructure Funding Statement (April 2024) the need for additional primary health care, acute care, and mental health provision should be addressed by considering the use of Strategic CIL to support new facilities rather than through s106 planning obligations). The officer's comment is acceptable.

Response to public consultation - conclusion

18. Having considered the local responses to public consultation, Haringey Council has sought to secure various planning obligations, conditions and informatives in response to the issues raised. GLA officers have had regard to the above statutory and non-statutory responses to the public consultation process, where these raise material planning issues of strategic importance.

Update

19. Since consultation stage GLA officers have engaged in joint discussions with the applicant, the Council and TfL officers with a view to addressing the above matters. Furthermore, as part of the Council's draft decision on the case, various planning conditions and obligations have been secured. An update against the issues raised at consultation stage is set out below, having regard to responses to the public consultation.

Relevant policies and guidance

20. Since consultation stage the following are now material considerations:

- Draft National Planning Policy Framework issued on 16 December 2025.
- A Written Ministerial Statement regarding a package of targeted and temporary emergency support measures to drive up housebuilding in London was issued on the 23 October 2025 by the Secretary of State for Housing , Communities and Local Government. Following a period of consultation a final joint point Policy Statement with the Mayor of London 'Support for

Housebuilding in London package of support was published 25 March 2026' <https://www.gov.uk/government/publications/support-for-housebuilding-in-london-package-of-support>

- Support for Housebuilding LPG published 25 March 2026.

Land use principles

Loss of education use

21. At Stage 1 the loss of educational use ('Special Educational Needs' - SEN college known as 'John Dewey Specialist College/Area 51 Education' currently operating from the site) was assessed, and GLA officers advised the Council alternative premises should be secured as part of any planning permission, or else a strong rationale provided as to why the service is not needed in the borough.
22. The Council's committee report noted that the existing SEN college use does not provide the land uses (and general aims) of the site allocation which seeks employment and residential use on this site. However, the report stated that the Council recognises the importance of this educational facility and the need to ensure continuity of provision for its users and that the applicants are currently working proactively with the college to identify and secure a suitable alternative location that meets its operational and accessibility requirements. This matter is being actively progressed by the Council who have agreed to find a suitable alternative site prior to the commencement of the proposed development and that no demolition would be allowed to proceed unless and until an alternative premise is secured and this is secured by the Director's agreement letter. Thus, GLA officers are convinced the concern related to the loss of educational need is resolved satisfactorily.
23. Notwithstanding the above, the proposed redevelopment for the site would be in accordance with and contribute to the land use planning requirements of the site allocation (SA 19), which is, overall, for employment-led mixed-use development with residential, as well as achieving the required wider aims and objectives. Therefore, the redevelopment of the site to provide affordable housing and flexible workspace within a town centre and an OA is strongly supported in strategic planning terms. The development would provide 539sqm of commercial floorspace (of flexible uses) secured as affordable office workspace.

Equalities

24. Given the proposed loss of the existing educational use (Area 51 Education) and proximity to John Raphael House (a place of worship) the applicant provided an Equality Impact Assessment (EqIA). The Council has assessed the case and secured the proposed mitigation measures which included:
 - Alternative premises for the SEN use should be found in the borough. The Council is working with Area 51 Education to find suitable alternative premises by July 2026.
 - A construction management plan, outlining engagement with the adjacent place of worship, should be secured.
25. As a result, the Equalities concerns are resolved satisfactorily.

Affordable Housing

26. The proposal to deliver 150 affordable housing units (100% by HR) consisting of 100% (low-cost) social-rented homes is strongly supported and secured. The proposal would therefore contribute to a mixed and balanced community and make a significant contribution to the delivery of the Borough wide affordable housing target.

Design and heritage

27. No strategic design issues are identified. The detailed environmental information regarding daylight, sunlight and wind microclimate were reviewed by the Council and suitable mitigation measures are secured. In terms of fire safety, each residential tower would be served on all storeys by two stair cores, comprising a dedicated evacuation stair and a firefighting stair. The commercial workspace areas would also be provided with two escape stairs and an evacuation lift. All these measures are in line with Policies D12 and D5 and have been secured by conditions.
28. As assessed at Stage 1, the very low level of 'less than substantial' harm that could be caused to the settings of Alexandra Park (Registered Park and Garden) would be outweighed by the public benefits of the proposal, including the provision of 150 affordable housing, and affordable office workspace.
29. Although there would be a shortfall in the quantum of provision of play space, the applicant has agreed to make a financial contribution which would be put towards off-site provision. This is secured by a Directors' agreement letter.

Transport

30. At Stage 1 consultation, a number of strategic and local transport matters were identified, relating to bus stops and construction. The applicant has clarified that construction and servicing access will have a limited impact on the bus stops on Western Road, and with other active travel zone measures being provided as part of the development proposals and highway agreements being secured in the vicinity of the site, the impacts of the development are satisfactorily mitigated.
31. The Director's agreement letter will secure £160,000 towards Active Travel Zone improvements, including the implementation of a new cycle route and junction and signal works, £50,000 towards pedestrian wayfinding to/from the site, Highways and footway improvement works and Traffic Management Order amendments, a Car-Free Agreement, Car Club spaces and membership, a Car parking Management Plan, a Construction Demolition Plan, and site wide Travel Plan and monitoring. A number of conditions are secured, including a Crossrail 2 Detailed Design and Method Statement, delivery and servicing management plan, cycle parking, and accessible parking.
32. Taking account of the assessment undertaken by the Council and the resolved conditions, and obligations secured through a Director's agreement letter, officers are satisfied that the application scheme is in general accordance with the transport policies in the London Plan and is acceptable in strategic transport terms.

Environment

33. The overall predicted reduction in CO₂ emissions for the development shows an improvement of approximately 66% in carbon emissions with SAP10.2 carbon factors, from the Baseline development model (which is Part L 2021 compliant). This represents an annual saving of approximately 89.43 tonnes of CO₂ from a baseline of 135.39 tCO₂/year. Carbon offset contribution is secured via the Director's agreement letter. Overall, the side-wide Whole Life Carbon meets GLA's target. The applicant is required to submit a postconstruction assessment to report on the development's actual whole life carbon emissions, which is secured by a condition. In terms of circular economy, there are some areas where additional information is required to confirm how the proposal will achieve GLA targets. The Council is satisfied this can be adequately addressed at a later stage, and as such this matter is secured by condition.
34. Other environmental issues including urban greening and biodiversity, sustainable drainage, water use, noise and air quality have been acceptably addressed, and proposed measures conditioned.

The Director's agreement letter

35. The Director's agreement letter includes the following provisions:
- It is noted that the Director's agreement letter signed between the parties (applicant as the Housing Department and Planning & Building Standards as the Local Planning Authority) secured obligations that would otherwise ordinarily be set out in a S106 agreement document. There is a mechanism in place to secure these obligations in the event of the transfer of the Property or part of the Property from the Council to another party.
 - Affordable homes - All the homes are secured as Social Rent properties.
 - Provision of children's play space within the development and contribution of £131,765 towards off-site provision, including the creation of new children's play space or improvements to existing provision in the locality.
 - Provision of affordable workspace with flexible uses in commercial space at ground and first floor.
 - Reprovision of Area 51 Education - Measures to prevent the redevelopment of the site taking place until suitable alternative accommodation has been provided.
 - Estimated carbon offset contribution (and associated obligations) of £130,987 (indicative), plus a 10% management fee.
 - Contribution of £160,000 towards Active Travel Zone improvements, including the implementation of a new cycle route and junction and signal works, and Highways and footway improvement works. Car-Capped Agreement, including a £4,000 contribution to amend the Traffic Management Order.
 - Contribution of £15,000 towards monitoring of the Construction Logistics and Management Plan, and Monitoring of commercial travel plan and Residential Travel Plan contribution of £15,000 per year, and £50,000 towards the development and installation of wayfinding signage,
 - Contribution of £136,270 towards planting of new standard sized trees within a 500-metre radius of the site to mitigate the CAVAT loss of the mature London Plane Trees proposed for removal.

Legal considerations

36. Under the arrangements set out in Article 5 of the Town and Country Planning (Mayor of London) Order 2008 the Mayor has the power under Article 6 to direct the local planning authority to refuse permission for a planning application referred to him under Article 4 of the Order. Mayor also has the power under Article 7 to direct that he will become the local planning authority for the purposes of determining the application. The Mayor may also leave the decision to the local authority. In directing refusal, the Mayor must have regard to the matters set out in Article 6(2) of the Order, including the principal purposes of the Greater London Authority, the effect on health and sustainable development, national policies and international obligations, regional planning guidance, and the use of the River Thames. The Mayor may direct refusal if he considers that to grant permission would be contrary to good strategic planning in Greater London. If he decides to direct refusal, the Mayor must set out his reasons, and the local planning authority must issue these with the refusal notice. If the Mayor decides to direct that he is to be the local planning authority, he must have regard to the matters set out in Article 7(3) and set out his reasons in the direction.

Financial considerations

37. Should the Mayor direct refusal, he would be the principal party at any subsequent appeal hearing or public inquiry. Government guidance emphasises that parties usually pay their own expenses arising from an appeal. Following an inquiry caused by a direction to refuse, costs may be awarded against the Mayor if he has either directed refusal unreasonably; handled a referral from a planning authority unreasonably; or, behaved unreasonably during the appeal. A major factor in deciding whether the Mayor has acted unreasonably will be the extent to which he has taken account of established planning policy.

Conclusion

38. The strategic issues raised at consultation stage with respect to the land use principles, affordable housing, design and heritage, transport, environment and sustainable infrastructure have been acceptably resolved on balance, and having regard to the details of the application, the matters set out in the committee report and the Council's draft decision, and considering the material planning considerations of strategic importance raised in responses to the public consultation, the application is acceptable in strategic planning terms, and there are no sound planning reasons for the Mayor to intervene in this case. It is therefore recommended that Haringey Council is advised to determine the case itself, subject to any action that the Secretary of State may take.

For further information, contact GLA Planning Unit (Development Management Team):

Tefera Tibebe, Strategic Planner (case officer)

email: tefera.tibebe@london.gov.uk

We are committed to being anti-racist, planning for a diverse and inclusive London and engaging all communities in shaping their city.